Project Title : REVISED SUBMISSION DRG FOR THE MAP NO-LDA/LD/22-23/2397 LAY OUT PLOTTED DEVELOPMENT FOR PLOT NO:- GH-3, SECTOR -H, HIGH TECH TOWNSHIP , SUSHANT GOLF CITY , LUCKNOWOWNER :- M/S PARDOS DEVELOPERS PVT. LTD.

File No	LDA/LD/23-24/3009	Sheet	1 / 4
Submission Date	2023-11-17	Scale	1:100

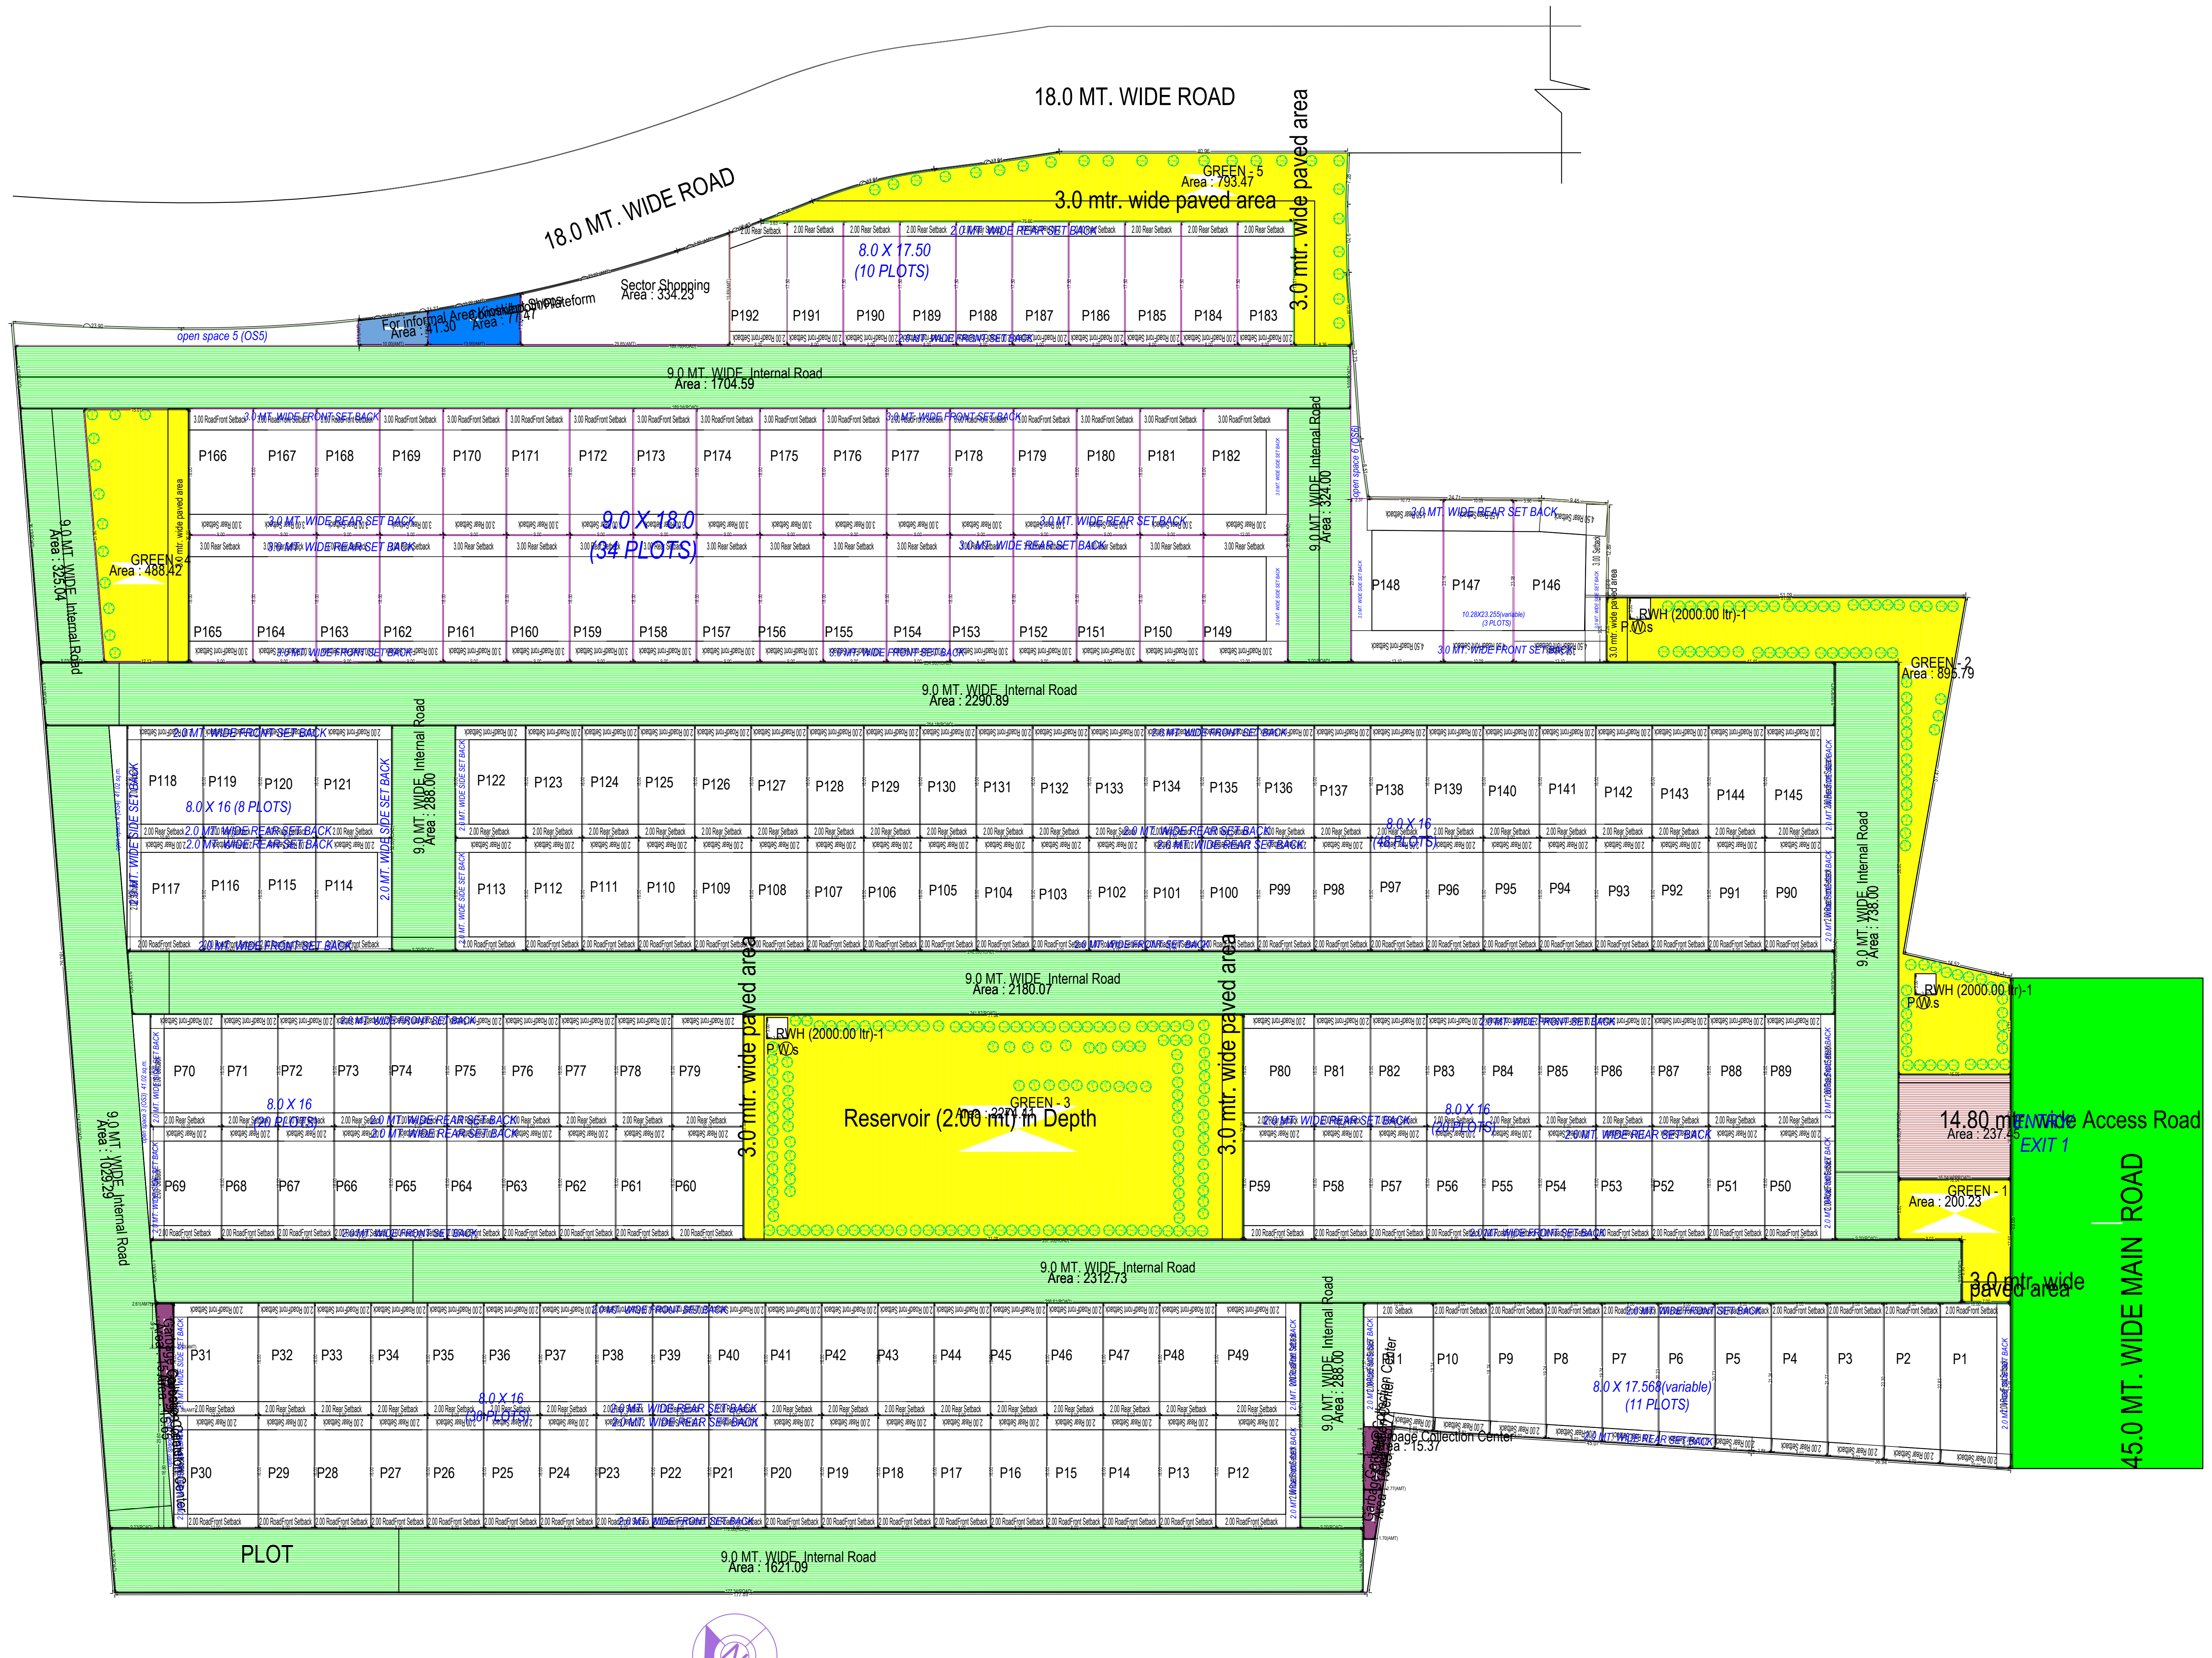
18.0 MT. WIDE ROAD
18.0 MT. WIDE ROAD
3.0 mtr. wide paved area
GREEN - 5
Area : 793.47
8.0 X 17.50
(10 PLOTS)
Sector Shopping
Area : 334.23
For informal Area
open space 5 (OSS)
9.0 MT. WIDE Internal Road
Area : 1704.59
9.0 X 18.0
(34 PLOTS)
GREEN
Area : 488.42
9.0 MT. WIDE Internal Road
Area : 2290.89
8.0 X 16 (8 PLOTS)
GREEN - 2
Area : 895.79
RWH (2000.00 ltr)-1
9.0 MT. WIDE Internal Road
Area : 2180.07
GREEN - 3
Reservoir (2.00 mt) in Depth
14.80 mt. Wide Access Road
EXIT 1
GREEN - 1
Area : 200.23
45.0 MT. WIDE MAIN ROAD
3.0 mtr. wide paved area
9.0 MT. WIDE Internal Road
Area : 2312.73
8.0 X 16
8.0 X 17.56(variable)
(11 PLOTS)
Garbage Collection Center
PLOT
9.0 MT. WIDE Internal Road
Area : 1821.09

LAYOUT PLAN
(Scale - 1:1000)

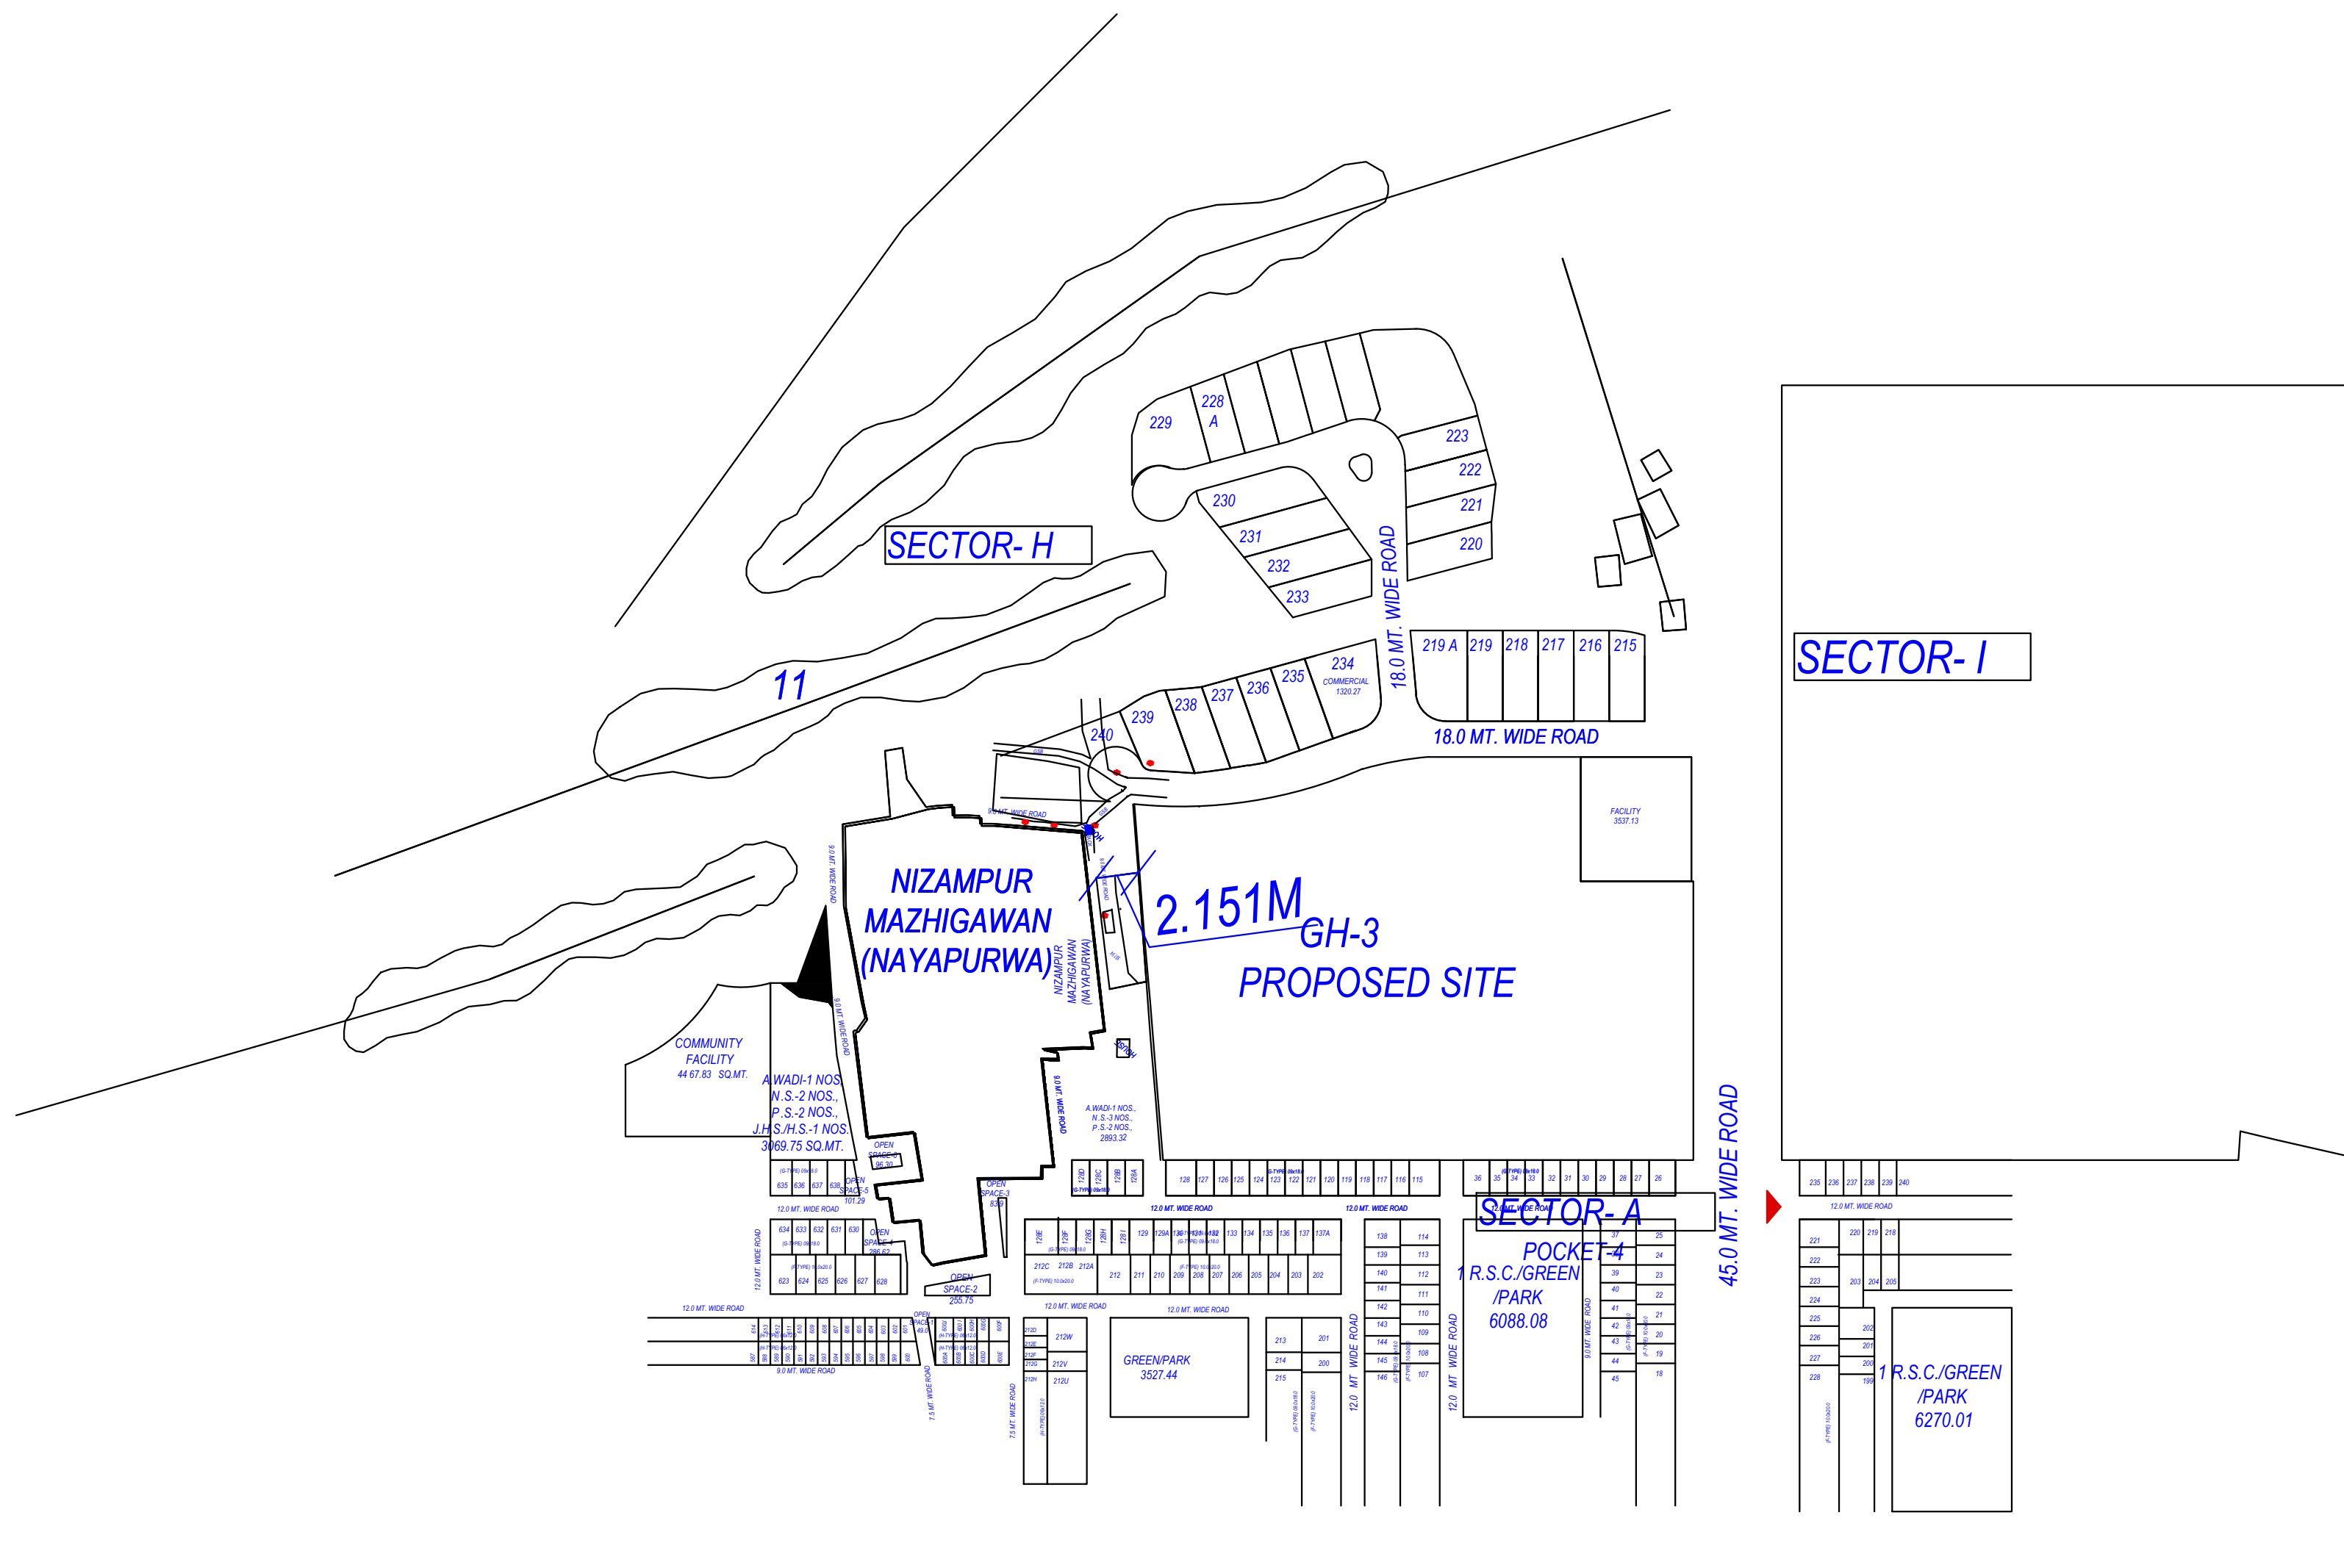
SECTOR- H
SECTOR- I
18.0 MT. WIDE ROAD
NIZAMPUR
MAZHIGAWAN
(NAYAPURWA)
2.151M
GH-3
PROPOSED SITE
SECTOR- A
45.0 MT. WIDE ROAD

KEY PLAN
(NOT TO SCALE)

Tree Details (Table 3h)

Plot	Name	Nos Of Trees	
		Reqd	Prop
PLOT	Tree	-	274

A	AREA STATEMENT	VERSION NO.: 1.0.89 VERSION DATE: 01/11/2023
	PROJECT DETAIL :	
	Authority: Lucknow Development Authority	Plot Use: Residential
	AuthorityClass: Category A	Plot SubUse: Plotted Resi development / Plotted Housing
	AuthorityGrade: Development Authority (DA)	Development Plan: API Ansal Sushant City
	CaseTrack: Regular	Land Use Zone: Residential use Zone
	Project Type: Layout Development	Land SubUse Zone: Residential Zone
	Nature of Development: NEW	Layout Type: NA
	Casetype: Revision	
	Development Area: New Area	
	SubDevelopment Area: Metro City Area	
	Special Project: NA	
	Site Address: District:Lucknow, Tehsil:Lucknow, Village:NA	
	AREA DETAILS :	Sq.Mts.
1.	Area of Plot As per record	-
	Document Area	46492.21
	As per site condition	46492.23
	Area of Plot Considered	46492.21
2.	Deduction for	
	(a)Proposed roads	0.00
	(b)Any reservations	0.00
	Total(a + b)	0.00
3.	Net Area of plot (1 - 2) AREA OF PLOT	46492.21
	Green and open space	4568.74
	Plot Area For Coverage	46492.21
	Plot Area For FSI	46492.21
	Perm. FSI Area (2.00)	92984.42
	Total Perm. FSI area (2.00)	92984.42
6.	Total Built up area permissible at:	
	Permissible Coverage area (65.00 %)	30219.94
	Proposed Coverage Area (- %)	0.00
	Total Prop. Coverage Area (- %)	0.00
	Balance coverage area (65.00 %)	30219.94
	Proposed Area at:	

-		Proposed Built up	Existing Built up	Proposed F.S.I	Existing F.S.I
	Total Area:	0.00	0.00	0.00	0.00

	Total FSI Area:	0.00
	AccessoryUse Area Added in BuiltUp Area:	27.00
	Total BuiltUp Area:	27.00
	Proposed F.S.I. consumed:	0.00
C.	Tenement Statement	
4.	Tenement Proposed At:	

Color Notes

COLOR INDEX	
PLOT BOUNDARY	■
ABUTTING ROAD	🟩
PROPOSED CONSTRUCTION	🟥
COMMON PLOT	🟨
ROAD ALIGNMENT (ROAD WIDENING AREA)	🟨
FUTURE T.P.SCHEME DEDUCTION AREA	🟦
EXISTING (To be retained)	🟦
EXISTING (To be demolished)	🟨

Land use analysis/Area distribution (Table 2c)

Area covered under	Proposed Area in sq. mt.	Percentage(%)
Plotted Area	27712.71	59.61
Road Area	13339.14	28.69
Garbage Collection Center	15.37	0.03
Garbage Collection Center	15.77	0.03
Garbage Collection Center	15.65	0.03
Garbage Collection Center	15.07	0.03
Garbage Collection Center	15.65	0.03
For informal Area Kiosk/booth/Plateform	41.30	0.09
Sector Shopping	334.23	0.72
Convinient Shops	77.47	0.17
Public Open Space	4568.74	9.83
Excess Paved Area	83.58	0.18
Other Area	257.54	0.55
Total net layout	46492.21	100.00

Number of EWS/LIG unit required

Sl. No.	Plot Type	Nos. of Plot	No. of unit in one plot	Total Number of units	Proposed LIG/EWS Unit
1.	Single Dwelling Unit	192	1	192	-
Total :		192		192	-
Number of EWS/LIG unit required (10% LIG)				20.00	0
Number of EWS/LIG unit required (10% EWS)				20.00	0
Total :		192		232	-

Tenements Density Check

Net housing density	No Of Tenements			No Of Persons		
	Reqd	Perm	Prop	Reqd	Perm	Prop
750/Hec.	-	698	518	-	3487	2590

Green and open space Area

Name	Prop. Area
GREEN - 3	2274.41
GREEN - 2	895.79
GREEN - 4	404.84
GREEN - 1	200.23
GREEN - 5	793.47

OWNER'S NAME AND SIGNATURE

PARDOUS DEVELOPERS PVT LTD, jschawla@ctc-lid.com, 9810571165

ARCH/ENG'S NAME AND SIGNA UCTURE ENGINEER

Rajneesh Kumar

CA/2017/86949

Signature Not Verified
Digitally signed by Rajneesh Kumar
Date: 22 Dec 2023 10:49:35
Designation :Architect

Lucknow Development Authority

Signature Not Verified
Digitally signed by INDRA MANI TRIPATHI
Date: 22 Dec 2023 19:21:14
Organization :Lucknow Development Authority
Designation :Vice Chairman

Building Plan Application Number
LDA/LD/23-24/3009

Sanctioned On
15 Dec 2023

Valid Till
21 Dec 2028

Approved By
Vice Chairman (Vice Chairman)

Examined By
Lakshman Singh (Junior engineer)
Atul Sharma (Junior engineer)
Rajesh Sharma (Assistant Engineer)
Atul Sharma (Junior engineer)
Rajesh Sharma (Assistant Engineer)
Atul Sharma (Junior engineer)

Note: - 1) This drawing is prepared as per the current prevailing Building Bye Laws.
2) If Map sanctioned is used for purpose anything other than stated in application will lead to rejection of Map.

Total Plot Area: - 46492.21	Total FAR Area: - 0.00
Total Coverage Area: - 0.00	Total BUA Area: - 0.00

ISO_A0_(841.00_x_1189.00_MM)

The correctness and accuracy of Proposal Information and drawing is a responsibilty of POR/owner. Accuracy of Scrutiny Report is subject to accuracy of end-user provided data, 3rd party software/hardware/services, etc. SoftTech Engineers Ltd. is not liable for any damages which may arise from use, or inability to use the Application. Texts printed in 'Italics' and 'Blue' color are user inputs, which are not verified and not generated by scrutiny software.

Proposed Population Calculation

Plot Name	Use	SubUse	Range	Nos.	Perm. Unit/Plot	Perm. Person/Unit	Total Person/Plot	Total
P10	Residential	Row House	above 50-upto 150sq.mt.	125	2	5	10	1250
P29	Residential	Row House			2		10	
P28	Residential	Row House			2		10	
P27	Residential	Row House			2		10	
P26	Residential	Row House			2		10	
P25	Residential	Row House			2		10	
P24	Residential	Row House			2		10	
P23	Residential	Row House			2		10	
P22	Residential	Row House			2		10	
P21	Residential	Row House			2		10	
P20	Residential	Row House			2		10	
P19	Residential	Row House			2		10	
P18	Residential	Row House			2		10	
P17	Residential	Row House			2		10	
P16	Residential	Row House			2		10	
P15	Residential	Row House			2		10	
P14	Residential	Row House			2		10	
P13	Residential	Row House			2		10	
P32	Residential	Row House			2		10	
P33	Residential	Row House			2		10	
P34	Residential	Row House			2		10	
P35	Residential	Row House			2		10	
P36	Residential	Row House			2		10	
P37	Residential	Row House			2		10	
P38	Residential	Row House			2		10	
P39	Residential	Row House			2		10	
P40	Residential	Row House			2		10	
P41	Residential	Row House			2		10	
P42	Residential	Row House			2		10	
P43	Residential	Row House			2		10	
P44	Residential	Row House			2		10	
P45	Residential	Row House			2		10	
P46	Residential	Row House			2		10	
P47	Residential	Row House			2		10	
P48	Residential	Row House			2		10	
P68	Residential	Row House			2		10	
P67	Residential	Row House			2		10	
P66	Residential	Row House			2		10	
P65	Residential	Row House			2		10	
P64	Residential	Row House			2		10	
P63	Residential	Row House			2		10	
P62	Residential	Row House			2		10	
P61	Residential	Row House			2		10	
P71	Residential	Row House			2		10	
P72	Residential	Row House			2		10	
P73	Residential	Row House			2		10	
P74	Residential	Row House			2		10	
P75	Residential	Row House			2		10	
P76	Residential	Row House			2		10	
P77	Residential	Row House			2		10	
P78	Residential	Row House			2		10	
P58	Residential	Row House			2		10	
P81	Residential	Row House			2		10	
P57	Residential	Row House			2		10	
P82	Residential	Row House			2		10	
P56	Residential	Row House			2		10	
P83	Residential	Row House			2		10	
P55	Residential	Row House			2		10	
P84	Residential	Row House			2		10	
P54	Residential	Row House			2		10	
P85	Residential	Row House			2		10	
P53	Residential	Row House			2		10	
P86	Residential	Row House			2		10	
P52	Residential	Row House			2		10	
P87	Residential	Row House			2		10	
P51	Residential	Row House			2		10	
P88	Residential	Row House			2		10	
P116	Residential	Row House			2		10	
P115	Residential	Row House			2		10	
P120	Residential	Row House			2		10	
P119	Residential	Row House			2		10	
P112	Residential	Row House			2		10	
P123	Residential	Row House			2		10	
P111	Residential	Row House			2		10	
P124	Residential	Row House			2		10	
P110	Residential	Row House			2		10	
P125	Residential	Row House			2		10	
P109	Residential	Row House			2		10	
P126	Residential	Row House			2		10	
P108	Residential	Row House			2		10	
P127	Residential	Row House			2		10	
P107	Residential	Row House			2		10	
P128	Residential	Row House			2		10	
P106	Residential	Row House			2		10	
P129	Residential	Row House			2		10	
P105	Residential	Row House			2		10	
P130	Residential	Row House			2		10	
P104	Residential	Row House			2		10	
P131	Residential	Row House			2		10	
P103	Residential	Row House			2		10	
P132	Residential	Row House			2		10	
P102	Residential	Row House			2		10	
P133	Residential	Row House			2		10	
P101	Residential	Row House			2		10	
P134	Residential	Row House			2		10	
P100	Residential	Row House			2		10	
P135	Residential	Row House			2		10	
P99	Residential	Row House			2		10	
P136	Residential	Row House			2		10	
P98	Residential	Row House			2		10	
P137	Residential	Row House			2		10	
P97	Residential	Row House			2		10	
P138	Residential	Row House			2		10	
P96	Residential	Row House			2		10	
P139	Residential	Row House			2		10	
P95	Residential	Row House			2		10	
P140	Residential	Row House			2		10	
P94	Residential	Row House			2		10	
P141	Residential	Row House			2		10	
P93	Residential	Row House			2		10	
P142	Residential	Row House			2		10	
P92	Residential	Row House			2		10	
P143	Residential	Row House			2		10	
P91	Residential	Row House			2		10	
P144	Residential	Row House			2		10	
P183	Residential	Row House			2		10	
P184	Residential	Row House			2		10	
P186	Residential	Row House			2		10	
P185	Residential	Row House			2		10	
P188	Residential	Row House			2		10	
P187	Residential	Row House			2		10	
P190	Residential	Row House			2		10	
P189	Residential	Row House			2		10	
P191	Residential	Row House			2		10	
P192	Residential	Row House			2		10	
P11	Residential	Row House	above 150-upto 300sq.mt	65	4	5	20	1300
P9	Residential	Row House			4		20	
P8	Residential	Row House			4		20	
P7	Residential	Row House			4		20	
P6	Residential	Row House			4		20	
P5	Residential	Row House			4		20	
P4	Residential	Row House			4		20	
P3	Residential	Row House			4		20	
P2	Residential	Row House			4		20	
P1	Residential	Row House			4		20	
P31	Residential	Row House			4		20	
P30	Residential	Row House			4		20	
P12	Residential	Row House			4		20	
P49	Residential	Row House			4		20	
P69	Residential	Row House			4		20	
P60	Residential	Row House			4		20	
P70	Residential	Row House			4		20	
P79	Residential	Row House			4		20	
P80	Residential	Row House			4		20	
P59	Residential	Row House			4		20	
P89	Residential	Row House			4		20	
P50	Residential	Row House			4		20	
P118	Residential	Row House			4		20	
P117	Residential	Row House			4		20	
P114	Residential	Row House			4		20	
P121	Residential	Row House			4		20	
P122	Residential	Row House			4		20	
P113	Residential	Row House			4		20	
P90	Residential	Row House			4		20	
P145	Residential	Row House			4		20	
P164	Residential	Row House			4		20	
P165	Residential	Row House			4		20	
P162	Residential	Row House			4		20	
P163	Residential	Row House			4		20	
P160	Residential	Row House			4		20	
P161	Residential	Row House			4		20	
P158	Residential	Row House			4		20	
P159	Residential	Row House			4		20	
P156	Residential	Row House			4		20	
P157	Residential	Row House			4		20	
P154	Residential	Row House			4		20	
P155	Residential	Row House			4		20	
P152	Residential	Row House			4		20	
P153	Residential	Row House			4		20	
P150	Residential	Row House			4		20	
P151	Residential	Row House			4		20	
P182	Residential	Row House			4		20	
P149	Residential	Row House			4		20	
P180	Residential	Row House			4		20	
P181	Residential	Row House			4		20	
P178	Residential	Row House			4		20	
P179	Residential	Row House			4		20	
P176	Residential	Row House			4		20	
P177	Residential	Row House			4		20	
P175	Residential	Row House			4		20	
P173	Residential	Row House			4		20	
P174	Residential	Row House			4		20	
P172	Residential	Row House			4		20	
P171	Residential	Row House			4		20	
P170	Residential	Row House			4		20	
P169	Residential	Row House			4		20	
P166	Residential	Row House			4		20	
P167	Residential	Row House			4		20	
P168	Residential	Row House			4		20	
P147	Residential	Row House			4		20	
P148	Residential	Row House	above 300-upto 399.999sq.mt	2	4	5	20	40
P146	Residential	Row House			4		20	
Grand Total:								2590

Individual Plot Area

Plot No.	Abutting Road	Plot Area			Frontage		Coverage			FSI Area	
		Reqd	Perm	Prop	Reqd	Prop	Factor	Perm	Prop	Perm	Prop
P11	9.0 MT. WIDE Internal Road	40.00	-	177.67	3.50	17.57	0.00	0.00	0.00	-	0.00
P10	9.0 MT. WIDE Internal Road	40.00	-	147.97	3.50	8.00	0.00	0.00	0.00	-	0.00
P9	9.0 MT. WIDE Internal Road	40.00	-	151.94	3.50	8.00	0.00	0.00	0.00	-	0.00
P8	9.0 MT. WIDE Internal Road	40.00	-	155.91	3.50	8.00	0.00	0.00	0.00	-	0.00
P7	9.0 MT. WIDE Internal Road	40.00	-	159.87	3.50	8.00	0.00	0.00	0.00	-	0.00
P6	9.0 MT. WIDE Internal Road	40.00	-	163.84	3.50	8.00	0.00	0.00	0.00	-	0.00
P5	9.0 MT. WIDE Internal Road	40.00	-	167.83	3.50	8.00	0.00	0.00	0.00	-	0.00
P4	9.0 MT. WIDE Internal Road	40.00	-	172.02	3.50	8.00	0.00	0.00	0.00	-	0.00
P3	9.0 MT. WIDE Internal Road	40.00	-	176.27	3.50	8.00	0.00	0.00	0.00	-	0.00
P2	9.0 MT. WIDE Internal Road	40.00	-	180.52	3.50	8.00	0.00	0.00	0.00	-	0.00
P1	45.0 MT. WIDE MAIN ROAD	40.00	-	231.43	3.50	23.49	0.00	0.00	0.00	-	0.00
P31	9.0 MT. WIDE Internal Road	40.00	-	192.00	3.50	12.00	0.00	0.00	0.00	-	0.00
P30	9.0 MT. WIDE Internal Road	40.00	-	192.00	3.50	12.00	0.00	0.00	0.00	-	0.00
P29	9.0 MT. WIDE Internal Road	40.00	-	128.00	3.50	8.00	0.00	0.00	0.00	-	0.00
P28	9.0 MT. WIDE Internal Road	40.00	-	128.00	3.50	8.00	0.00	0.00	0.00	-	0.00
P27	9.0 MT. WIDE Internal Road	40.00	-	128.00	3.50	8.00	0.00	0.00	0.00	-	0.00
P26	9.0 MT. WIDE Internal Road	40.00	-	128.00	3.50	8.00	0.00	0.00	0.00	-	0.00
P25	9.0 MT. WIDE Internal Road	40.00	-	128.00	3.50	8.00	0.00	0.00	0.00	-	0.00
P24	9.0 MT. WIDE Internal Road	40.00	-	128.00	3.50	8.00	0.00	0.00	0.00	-	0.00
P23	9.0 MT. WIDE Internal Road	40.00	-	128.00	3.50	8.00	0.00	0.00	0.00	-	0.00
P22	9.0 MT. WIDE Internal Road	40.00	-	128.00	3.50	8.00	0.00	0.00	0.00	-	0.00
P21	9.0 MT. WIDE Internal Road	40.00	-	128.00	3.50	8.00	0.00	0.00	0.00	-	0.00
P20	9.0 MT. WIDE Internal Road	40.00	-	128.00	3.50	8.00	0.00	0.00	0.00	-	0.00
P19	9.0 MT. WIDE Internal Road	40.00	-	128.00	3.50	8.00	0.00	0.00	0.00	-	0.00
P18	9.0 MT. WIDE Internal Road	40.00	-	128.00	3.50	8.00	0.00	0.00	0.00	-	0.00
P17	9.0 MT. WIDE Internal Road	40.00	-	128.00	3.50	8.00	0.00	0.00	0.00	-	0.00
P16	9.0 MT. WIDE Internal Road	40.00	-	128.00	3.50	8.00	0.00	0.00	0.00	-	0.00
P15	9.0 MT. WIDE Internal Road	40.00	-	128.00	3.50	8.00	0.00	0.00	0.00	-	0.00
P14	9.0 MT. WIDE Internal Road	40.00	-	128.00	3.50	8.00	0.00	0.00	0.00	-	0.00
P13	9.0 MT. WIDE Internal Road	40.00	-	128.00	3.50	8.00	0.00	0.00	0.00	-	0.00
P12	9.0 MT. WIDE Internal Road	40.00	-	192.00	3.50	28.00	0.00	0.00	0.00	-	0.00
P32	9.0 MT. WIDE Internal Road	40.00	-	128.00	3.50	8.00	0.00	0.00	0.00	-	0.00
P33	9.0 MT. WIDE Internal Road	40.00	-	128.00	3.50	8.00	0.00	0.00	0.00	-	0.00
P34	9.0 MT. WIDE Internal Road	40.00	-	128.00	3.50	8.00	0.00	0.00	0.00	-	0.00
P35	9.0 MT. WIDE Internal Road	40.00	-	128.00	3.50	8.00	0.00	0.00	0.00	-	0.00
P36	9.0 MT. WIDE Internal Road	40.00	-	128.00	3.50	8.00	0.00	0.00	0.00	-	0.00
P37	9.0 MT. WIDE Internal Road	40.00	-	128.00	3.50	8.00	0.00	0.00	0.00	-	0.00
P38	9.0 MT. WIDE Internal Road	40.00	-	128.00	3.50	8.00	0.00	0.00	0.00	-	0.00
P39	9.0 MT. WIDE Internal Road	40.00	-	128.00	3.50	8.00	0.00	0.00	0.00	-	0.00
P40	9.0 MT. WIDE Internal Road	40.00	-	128.00	3.50	8.00	0.00	0.00	0.00	-	0.00
P41	9.0 MT. WIDE Internal Road	40.00	-	128.00	3.50	8.00	0.00	0.00	0.00	-	0.00
P42	9.0 MT. WIDE Internal Road	40.00	-	128.00	3.50	8.00	0.00	0.00	0.00	-	0.00
P43	9.0 MT. WIDE Internal Road	40.00	-	128.00	3.50	8.00	0.00	0.00	0.00	-	0.00
P44	9.0 MT. WIDE Internal Road	40.00	-	128.00	3.50	8.00	0.00	0.00	0.00	-	0.00
P45	9.0 MT. WIDE Internal Road	40.00	-	128.00	3.50	8.00	0.00	0.00	0.00	-	0.00
P46	9.0 MT. WIDE Internal Road	40.00	-	128.00	3.50	8.00	0.00	0.00	0.00	-	0.00
P47	9.0 MT. WIDE Internal Road	40.00	-	128.00	3.50	8.00	0.00	0.00	0.00	-	0.00
P48	9.0 MT. WIDE Internal Road	40.00	-	128.00	3.50	8.00	0.00	0.00	0.00	-	0.00
P49	9.0 MT. WIDE Internal Road	40.00	-	192.00	3.50	16.00	0.00	0.00	0.00	-	0.00
P69	9.0 MT. WIDE Internal Road	40.00	-	161.60	3.50	10.10	0.00	0.00	0.00	-	0.00
P68	9.0 MT. WIDE Internal Road	40.00	-	128.00	3.50	8.00	0.00	0.00	0.00	-	0.00
P67	9.0 MT. WIDE Internal Road	40.00	-	128.00	3.50	8.00	0.00	0.00	0.00	-	0.00
P66	9.0 MT. WIDE Internal Road	40.00	-	128.00	3.50	8.00	0.00	0.00	0.00	-	0.00
P65	9.0 MT. WIDE Internal Road	40.00	-	128.00	3.50	8.00	0.00	0.00	0.00	-	0.00
P64	9.0 MT. WIDE Internal Road	40.00	-	128.00	3.50	8.00	0.00	0.00	0.00	-	0.00
P63	9.0 MT. WIDE Internal Road	40.00	-	128.00	3.50	8.00	0.00	0.00	0.00	-	0.00
P62	9.0 MT. WIDE Internal Road	40.00	-	128.00	3.50	8.00	0.00	0.00	0.00	-	0.00
P61	9.0 MT. WIDE Internal Road	40.00	-	128.00	3.50	8.00	0.00	0.00	0.00	-	0.00
P60	9.0 MT. WIDE Internal Road	40.00	-	161.60	3.50	10.10	0.00	0.00	0.00	-	0.00
P70	9.0 MT. WIDE Internal Road	40.00	-	161.60	3.50	10.10	0.00	0.00	0.00	-	0.00
P71	9.0 MT. WIDE Internal Road	40.00	-	128.00	3.50	8.00	0.00	0.00	0.00	-	0.00
P72	9.0 MT. WIDE Internal Road	40.00	-	128.00	3.50	8.00	0.00	0.00	0.00	-	0.00
P73	9.0 MT. WIDE Internal Road	40.00	-	128.00	3.50	8.00	0.00	0.00	0.00	-	0.00
P74	9.0 MT. WIDE Internal Road	40.00	-	128.00	3.50	8.00	0.00	0.00	0.00	-	0.00
P75	9.0 MT. WIDE Internal Road	40.00	-	128.00	3.50	8.00	0.00	0.00	0.00	-	0.00
P76	9.0 MT. WIDE Internal Road	40.00	-	128.00	3.50	8.00	0.00	0.00	0.00	-	0.00
P77	9.0 MT. WIDE Internal Road	40.00	-	128.00	3.50	8.00	0.00	0.00	0.00	-	0.00
P78	9.0 MT. WIDE Internal Road	40.00	-	128.00	3.50	8.00	0.00	0.00	0.00	-	0.00
P79	9.0 MT. WIDE Internal Road	40.00	-	161.60	3.50	10.10	0.00	0.00	0.00	-	0.00
P80	9.0 MT. WIDE Internal Road	40.00	-	160.00	3.50	10.00	0.00	0.00	0.00	-	0.00
P59	9.0 MT. WIDE Internal Road	40.00	-	160.00	3.50	10.00	0.00	0.00	0.00	-	0.00
P58	9.0 MT. WIDE Internal Road	40.00	-	128.00	3.50	8.00	0.00	0.00	0.00	-	0.00
P81	9.0 MT. WIDE Internal Road	40.00	-	128.00	3.50	8.00	0.00	0.00	0.00	-	0.00
P57	9.0 MT. WIDE Internal Road	40.00	-	128.00	3.50	8.00	0.00	0.00	0.00	-	0.00
P82	9.0 MT. WIDE Internal Road	40.00	-	128.00	3.50	8.00	0.00	0.00	0.00	-	0.00
P56	9.0 MT. WIDE Internal Road	40.00	-	128.00	3.50	8.00	0.00	0.00	0.00	-	0.00
P83	9.0 MT. WIDE Internal Road	40.00	-	128.00	3.50	8.00	0.00	0.00	0.00	-	0.00
P55	9.0 MT. WIDE Internal Road	40.00	-	128.00	3.50	8.00	0.00	0.00	0.00	-	0.00
P84	9.0 MT. WIDE Internal Road	40.00	-	128.00	3.50	8.00	0.00	0.00	0.00	-	0.00
P54	9.0 MT. WIDE Internal Road	40.00	-	128.00	3.50	8.00	0.00	0.00	0.00	-	0.00
P85	9.0 MT. WIDE Internal Road	40.00	-	128.00	3.50	8.00	0.00	0.00	0.00	-	0.00
P53	9.0 MT. WIDE Internal Road	40.00	-	128.00	3.50	8.00	0.00	0.00	0.00	-	0.00
P86	9.0 MT. WIDE Internal Road	40.00	-	128.00	3.50	8.00	0.00	0.00	0.00	-	0.00
P52	9.0 MT. WIDE Internal Road	40.00	-	128.00	3.50	8.00	0.00	0.00	0.00	-	0.00
P87	9.0 MT. WIDE Internal Road	40.00	-	128.00	3.50	8.00	0.00	0.00	0.00	-	0.00
P51	9.0 MT. WIDE Internal Road	40.00	-	128.00	3.50	8.00	0.00	0.00	0.00	-	0.00
P88	9.0 MT. WIDE Internal Road	40.00	-	128.00	3.50	8.00	0.00	0.00	0.00	-	0.00
P89	9.0 MT. WIDE Internal Road	40.00	-	160.00	3.50	26.00	0.00	0.00	0.00	-	0.00
P50	9.0 MT. WIDE Internal Road	40.00	-	160.00	3.50	26.00	0.00	0.00	0.00	-	0.00
P118	9.0 MT. WIDE Internal Road	40.00	-	172.72	3.50	10.80	0.00	0.00	0.00	-	0.00
P117	9.0 MT. WIDE Internal Road	40.00	-	172.72	3.50	10.80	0.00	0.00	0.00	-	0.00
P116	9.0 MT. WIDE Internal Road	40.00	-	128.00	3.50	8.00	0.00	0.00	0.00	-	0.00
P115	9.0 MT. WIDE Internal Road	40.00	-	128.00	3.50	8.00	0.00	0.00	0.00	-	0.00
P114	9.0 MT. WIDE Internal Road	40.00	-	172.72	3.50	26.80	0.00	0.00	0.00	-	0.00
P121	9.0 MT. WIDE Internal Road	40.00	-	172.72	3.50	26.80	0.00	0.00	0.00	-	0.00
P120	9.0 MT. WIDE Internal Road	40.00	-	128.00	3.50	8.00	0.00	0.00	0.00	-	0.00
P119	9.0 MT. WIDE Internal Road	40.00	-	128.00	3.50	8.00	0.00	0.00	0.00	-	0.00
P122	9.0 MT. WIDE Internal Road	40.00	-	160.00	3.50	26.00	0.00	0.00	0.00	-	0.00
P113	9.0 MT. WIDE Internal Road	40.00	-	160.00	3.50	26.00	0.00	0.00	0.00	-	0.00
P112	9.0 MT. WIDE Internal Road	40.00	-	128.00	3.50	8.00	0.00	0.00	0.00	-	0.00
P123	9.0 MT. WIDE Internal Road	40.00	-	128.00	3.50	8.00	0.00	0.00	0.00	-	0.00
P111	9.0 MT. WIDE Internal Road	40.00	-	128.00	3.50	8.00	0.00	0.00	0.00	-	0.00
P124	9.0 MT. WIDE Internal Road	40.00	-	128.00	3.50	8.00	0.00	0.00	0.00	-	0.00
P110	9.0 MT. WIDE Internal Road	40.00	-	128.00	3.50	8.00	0.00	0.00	0.00	-	0.00
P125	9.0 MT. WIDE Internal Road	40.00	-	128.00	3.50	8.00	0.00	0.00	0.00	-	0.00
P109	9.0 MT. WIDE Internal Road	40.00	-	128.00	3.50	8.00	0.00	0.00	0.00	-	0.00
P126	9.0 MT. WIDE Internal Road	40.00	-	128.00	3.50	8.00	0.00	0.00	0.00	-	0.00
P108	9.0 MT. WIDE Internal Road	40.00	-	128.00	3.50	8.00	0.00	0.00	0.00	-	0.00
P127	9.0 MT. WIDE Internal Road	40.00	-	128.00	3.50	8.00	0.00	0.00	0.00	-	0.00
P107	9.0 MT. WIDE Internal Road	40.00	-	128.00	3.50	8.00	0.00	0.00	0.00	-	0.00
P128	9.0 MT. WIDE Internal Road	40.00	-	128.00	3.50	8.00	0.00	0.00	0.00	-	0.00
P106	9.0 MT. WIDE Internal Road	40.00	-	128.00	3.50	8.00	0.00	0.00	0.00	-	0.00
P129	9.0 MT. WIDE Internal Road	40.00	-	128.00	3.50	8.00	0.00	0.00	0.00	-	0.00
P105	9.0 MT. WIDE Internal Road	40.00	-	128.00	3.50	8.00	0.00	0.00	0.00	-	0.00
P130	9.0 MT. WIDE Internal Road	40.00	-	128.00	3.50	8.00	0.00	0.00	0.00	-	0.00
P104	9.0 MT. WIDE Internal Road	40.00	-	128.00	3.50	8.00	0.00	0.00	0.00	-	0.00
P131	9.0 MT. WIDE Internal Road	40.00	-	128.00	3.50	8.00	0.00	0.00	0.00	-	0.00
P103	9.0 MT. WIDE Internal Road	40.00	-	128.00	3.50	8.00	0.00	0.00	0.00	-	0.00
P132	9.0 MT. WIDE Internal Road	40.00	-	128.00	3.50	8.00	0.00	0.00	0.00	-	0.00
P102	9.0 MT. WIDE Internal Road	40.00	-	128.00	3.50	8.00	0.00	0.00	0.00	-	0.00
P133	9.0 MT. WIDE Internal Road	40.00	-	128.00	3.50	8.00	0.00	0.00	0.00	-	0.00
P101	9.0 MT. WIDE Internal Road	40.00	-	128.00	3.50	8.00	0.00	0.00	0.00	-	0.00
P134	9.0 MT. WIDE Internal Road	40.00	-	128.00	3.50	8.00	0.00	0.00	0.00	-	0.00
P100	9.0 MT. WIDE Internal Road	40.00	-	128.00	3.50	8.00	0.00	0.00	0.00	-	0.00
P135	9.0 MT. WIDE Internal Road	40.00	-	128.00	3.50	8.00	0.00	0.00	0.00	-	0.00
P99	9.0 MT. WIDE Internal Road	40.00	-	128.00	3.50	8.00	0.00	0.00	0.00	-	0.00
P136	9.0 MT. WIDE Internal Road	40.00	-	128.00	3.50	8.00	0.00	0.00	0.00	-	0.00
P98	9.0 MT. WIDE Internal Road	40.00	-	128.00	3.50	8.00	0.00	0.00	0.00	-	0.00
P137	9.0 MT. WIDE Internal Road	40.00	-	128.00	3.50	8.00	0.00	0.00	0.00	-	0.00
P97	9.0 MT. WIDE Internal Road	40.00	-	128.00	3.50	8.00	0.00	0.00	0.00	-	0.00
P138	9.0 MT. WIDE Internal Road	40.00	-	128.00	3.50	8.00	0.00	0.00	0.00	-	0.00
P96	9.0 MT. WIDE Internal Road	40.00	-	128.00	3.50	8.00	0.00	0.00	0.00	-	0.00
P139	9.0 MT. WIDE Internal Road	40.00	-	128.00	3.50	8.00	0.00	0.00	0.00	-	0.00
P95	9.0 MT. WIDE Internal Road	40.00	-	128.00	3.50	8.00	0.00	0.00	0.00	-	0.00
P140	9.0 MT. WIDE Internal Road	40.00	-	128.00	3.50	8.00	0.00	0.00	0.00	-	0.00
P94	9.0 MT. WIDE Internal Road	40.00	-	128.00	3.50	8.00	0.00	0.00	0.00	-	0.00
P141	9.0 MT. WIDE Internal Road	40.00	-	128.00	3.50	8.00	0.00	0.00	0.00	-	0.00
P93	9.0 MT. WIDE Internal Road	40.00	-	128.00	3.50	8.00	0.00	0.00	0.00	-	0.00
P142	9.0 MT. WIDE Internal Road	40.00	-	128.00	3.50	8.00	0.00	0.00	0.00	-	0.00
P92	9.0 MT. WIDE Internal Road	40.00	-	128.00	3.50	8.00	0.00	0.00	0.00	-	0.00
P143	9.0 MT. WIDE Internal Road	40.00	-	128.00	3.50	8.00	0.00	0.00	0.00	-	0.00
P91	9.0 MT. WIDE Internal Road	40.00	-	128.00	3.50	8.00	0.00	0.00	0.00	-	0.00
P144	9.0 MT. WIDE Internal Road	40.00	-	128.00	3.50	8.00	0.00	0.00	0.00	-	0.00
P90	9.0 MT. WIDE Internal Road	40.00	-	160.00	3.50	26.00	0.00	0.00	0.00	-	0.00
P145	9.0 MT. WIDE Internal Road	40.00	-	160.00	3.50	26.00	0.00	0.00	0.00	-	0.00
P164	9.0 MT. WIDE Internal Road	40.00	-	162.00	3.50	9.00	0.00	0.00	0.00	-	0.00
P165	9.0 MT. WIDE Internal Road	40.00	-	162.00	3.50	9.00	0.00	0.00	0.00	-	0.00
P162	9.0 MT. WIDE Internal Road	40.00	-	162.00	3.50	9.00	0.00	0.00	0.00	-	0.00
P163	9.0 MT. WIDE Internal Road	40.00	-	162.00	3.50	9.00	0.00	0.00	0.00	-	0.00
P160	9.0 MT. WIDE Internal Road	40.00	-	162.00	3.50	9.00	0.00	0.00	0.00	-	0.00
P161	9.0 MT. WIDE Internal Road	40.00	-	162.00	3.50	9.00	0.00	0.00	0.00	-	0.00
P158	9.0 MT. WIDE Internal Road	40.00	-	162.00	3.50	9.00	0.00	0.00	0.00	-	0.00
P159	9.0 MT. WIDE Internal Road	40.00	-	162.00	3.50	9.00	0.00	0.00	0.00	-	0.00
P156	9.0 MT. WIDE Internal Road	40.00	-	162.00	3.50	9.00	0.00	0.00	0.00	-	0.00
P157	9.0 MT. WIDE Internal Road	40.00	-	162.00	3.50	9.00	0.00	0.00	0.00	-	0.00
P154	9.0 MT. WIDE Internal Road	40.00	-	162.00	3.50	9.00	0.00	0.00	0.00	-	0.00
P155	9.0 MT. WIDE Internal Road	40.00	-	162.00	3.50	9.00	0.00	0.00	0.00	-	0.00
P152	9.0 MT. WIDE Internal Road	40.00	-	162.00	3.50	9.00	0.00	0.00	0.00	-	0.00
P153	9.0 MT. WIDE Internal Road	40.00	-	162.00	3.50	9.00	0.00	0.00	0.00	-	0.00
P150	9.0 MT. WIDE Internal Road	40.00	-	162.00	3.50	9.00	0.00	0.00	0.00	-	0.00
P151	9.0 MT. WIDE Internal Road	40.00	-	162.00	3.50	9.00	0.00	0.00	0.00	-	0.00
P182	9.0 MT. WIDE Internal Road	40.00	-	216.00	3.50	30.00	0.00	0.00	0.00	-	0.00
P149	9.0 MT. WIDE Internal Road	40.00	-	216.00	3.50	30.00	0.00	0.00	0.00	-	0.00
P180	9.0 MT. WIDE Internal Road	40.00	-	162.00	3.50	9.00	0.00	0.00	0.00	-	0.00
P181	9.0 MT. WIDE Internal Road	40.00	-	162.00	3.50	9.00	0.00	0.00	0.00	-	0.00
P178	9.0 MT. WIDE Internal Road	40.00	-	162.00	3.50	9.00	0.00	0.00	0.00	-	0.00
P179	9.0 MT. WIDE Internal Road	40.00	-	162.00	3.50	9.00	0.00	0.00	0.00	-	0.00
P176	9.0 MT. WIDE Internal Road	40.00	-	162.00	3.50	9.00	0.00	0.00	0.00	-	0.00
P177	9.0 MT. WIDE Internal Road	40.00	-	162.00	3.50	9.00	0.00	0.00	0.00	-	0.00
P175	9.0 MT. WIDE Internal Road	40.00	-	162.00	3.50	9.00	0.00	0.00	0.00	-	0.00
P173	9.0 MT. WIDE Internal Road	40.00	-	162.00	3.50	9.00	0.00	0.00	0.00	-	0.00
P174	9.0 MT. WIDE Internal Road	40.00	-	162.00	3.50	9.00	0.00	0.00	0.00	-	0.00
P172	9.0 MT. WIDE Internal Road	40.00	-	162.00	3.50	9.00	0.00	0.00	0.00	-	0.00
P171	9.0 MT. WIDE Internal Road	40.00	-	162.00	3.50	9.00	0.00	0.00	0.00	-	0.00
P170	9.0 MT. WIDE Internal Road	40.00	-	162.00	3.50	9.00	0.00	0.00	0.00	-	0.00
P169	9.0 MT. WIDE Internal Road	40.00	-	162.00	3.50	9.00	0.00	0.00	0.00	-	0.00
P166	9.0 MT. WIDE Internal Road	40.00	-	162.00	3.50	9.00	0.00	0.00	0.00	-	0.00
P167	9.0 MT. WIDE Internal Road	40.00	-	162.00	3.50	9.00	0.00	0.00	0.00	-	0.00
P168	9.0 MT. WIDE Internal Road	40.00	-	162.00	3.50	9.00	0.00	0.00	0.00	-	0.00
P183	9.0 MT. WIDE Internal Road	40.00	-	140.00	3.50	8.00	0.00	0.00	0.00	-	0.00
P184	9.0 MT. WIDE Internal Road	40.00	-	140.00	3.50	8.00	0.00	0.00	0.00	-	0.00
P186	9.0 MT. WIDE Internal Road	40.00	-	140.00	3.50	8.00	0.00	0.00	0.00	-	0.00
P185	9.0 MT. WIDE Internal Road	40.00	-	140.00	3.50	8.00	0.00	0.00	0.00	-	0.00
P188	9.0 MT. WIDE Internal Road	40.00	-	140.00	3.50	8.00	0.00	0.00	0.00	-	0.00
P187	9.0 MT. WIDE Internal Road	40.00	-	140.00	3.50	8.00	0.00	0.00	0.00	-	0.00
P190	9.0 MT. WIDE Internal Road	40.00	-	140.00	3.50	8.00	0.00	0.00	0.00	-	0.00
P189	9.0 MT. WIDE Internal Road	40.00	-	140.00	3.50	8.00	0.00	0.00	0.00	-	0.00
P191	9.0 MT. WIDE Internal Road	40.00	-	140.00	3.50	8.00	0.00	0.00	0.00	-	0.00
P192	9.0 MT. WIDE Internal Road	40.00	-	136.46	3.50	8.00	0.00	0.00	0.00	-	0.00
P147	9.0 MT. WIDE Internal Road	40.00	-	233.17	3.50	10.09	0.00	0.00	0.00	-	0.00
P148	9.0 MT. WIDE Internal Road	40.00	-	304.15	3.50	36.35	0.00	0.00	0.00	-	0.00
P146	9.0 MT. WIDE Internal Road	40.00	-	300.38	3.50	13.10	0.00	0.00	0.00	-	0.00

Individual Plot Setback

Plot No.	Pwork-Bldg	Abutting Road	Front		Side1		Side2		Rear		Coverage	FSI Area
			Reqd	Prop	Reqd	Prop	Reqd	Prop	Reqd	Prop	Prop	Prop
P11		9.0 MT. WIDE Internal Road	2.00	-	-	-	-	-	2.00	-	0.00	0.00
P11		9.0 MT. WIDE Internal Road	2.00	-	-	-	-	-	-	-	0.00	0.00
P10		9.0 MT. WIDE Internal Road	2.00	-	-	-	-	-	2.00	-	0.00	0.00
P9		9.0 MT. WIDE Internal Road	2.00	-	-	-	-	-	2.00	-	0.00	0.00
P8		9.0 MT. WIDE Internal Road	2.00	-	-	-	-	-	2.00	-	0.00	0.00
P7		9.0 MT. WIDE Internal Road	2.00	-	-	-	-	-	2.00	-	0.00	0.00
P6		9.0 MT. WIDE Internal Road	2.00	-	-	-	-	-	2.00	-	0.00	0.00
P5		9.0 MT. WIDE Internal Road	2.00	-	-	-	-	-	2.00	-	0.00	0.00
P4		9.0 MT. WIDE Internal Road	2.00	-	-	-	-	-	2.00	-	0.00	0.00
P3		9.0 MT. WIDE Internal Road	2.00	-	-	-	-	-	2.00	-	0.00	0.00
P2		9.0 MT. WIDE Internal Road	2.00	-	-	-	-	-	2.00	-	0.00	0.00
P1		9.0 MT. WIDE Internal Road	2.00	-	-	-	-	-	-	-	0.00	0.00
P1		45.0 MT. WIDE MAIN ROAD	2.00	-	-	-	-	-	2.00	-	0.00	0.00
P31		9.0 MT. WIDE Internal Road	2.00	-	-	-	-	-	2.00	-	0.00	0.00
P30		9.0 MT. WIDE Internal Road	2.00	-	-	-	-	-	2.00	-	0.00	0.00
P29		9.0 MT. WIDE Internal Road	2.00	-	-	-	-	-	2.00	-	0.00	0.00
P28		9.0 MT. WIDE Internal Road	2.00	-	-	-	-	-	2.00	-	0.00	0.00
P27		9.0 MT. WIDE Internal Road	2.00	-	-	-	-	-	2.00	-	0.00	0.00
P26		9.0 MT. WIDE Internal Road	2.00	-	-	-	-	-	2.00	-	0.00	0.00
P25		9.0 MT. WIDE Internal Road	2.00	-	-	-	-	-	2.00	-	0.00	0.00
P24		9.0 MT. WIDE Internal Road	2.00	-	-	-	-	-	2.00	-	0.00	0.00
P23		9.0 MT. WIDE Internal Road	2.00	-	-	-	-	-	2.00	-	0.00	0.00
P22		9.0 MT. WIDE Internal Road	2.00	-	-	-	-	-	2.00	-	0.00	0.00
P21		9.0 MT. WIDE Internal Road	2.00	-	-	-	-	-	2.00	-	0.00	0.00
P20		9.0 MT. WIDE Internal Road	2.00	-	-	-	-	-	2.00	-	0.00	0.00
P19		9.0 MT. WIDE Internal Road	2.00	-	-	-	-	-	2.00	-	0.00	0.00
P18		9.0 MT. WIDE Internal Road	2.00	-	-	-	-	-	2.00	-	0.00	0.00
P17		9.0 MT. WIDE Internal Road	2.00	-	-	-	-	-	2.00	-	0.00	0.00
P16		9.0 MT. WIDE Internal Road	2.00	-	-	-	-	-	2.00	-	0.00	0.00
P15		9.0 MT. WIDE Internal Road	2.00	-	-	-	-	-	2.00	-	0.00	0.00
P14		9.0 MT. WIDE Internal Road	2.00	-	-	-	-	-	2.00	-	0.00	0.00
P13		9.0 MT. WIDE Internal Road	2.00	-	-	-	-	-	2.00	-	0.00	0.00
P12		9.0 MT. WIDE Internal Road	2.00	-	-	-	-	-	2.00	-	0.00	0.00
P12		9.0 MT. WIDE Internal Road	2.00	-	-	-	-	-	-	-	0.00	0.00
P32		9.0 MT. WIDE Internal Road	2.00	-	-	-	-	-	2.00	-	0.00	0.00
P33		9.0 MT. WIDE Internal Road	2.00	-	-	-	-	-	2.00	-	0.00	0.00
P34		9.0 MT. WIDE Internal Road	2.00	-	-	-	-	-	2.00	-	0.00	0.00
P35		9.0 MT. WIDE Internal Road	2.00	-	-	-	-	-	2.00	-	0.00	0.00
P36		9.0 MT. WIDE Internal Road	2.00	-	-	-	-	-	2.00	-	0.00	0.00
P37		9.0 MT. WIDE Internal Road	2.00	-	-	-	-	-	2.00	-	0.00	0.00
P38		9.0 MT. WIDE Internal Road	2.00	-	-	-	-	-	2.00	-	0.00	0.00
P39		9.0 MT. WIDE Internal Road	2.00	-	-	-	-	-	2.00	-	0.00	0.00
P40		9.0 MT. WIDE Internal Road	2.00	-	-	-	-	-	2.00	-	0.00	0.00
P41		9.0 MT. WIDE Internal Road	2.00	-	-	-	-	-	2.00	-	0.00	0.00
P42		9.0 MT. WIDE Internal Road	2.00	-	-	-	-	-	2.00	-	0.00	0.00
P43		9.0 MT. WIDE Internal Road	2.00	-	-	-	-	-	2.00	-	0.00	0.00
P44		9.0 MT. WIDE Internal Road	2.00	-	-	-	-	-	2.00	-	0.00	0.00
P45		9.0 MT. WIDE Internal Road	2.00	-	-	-	-	-	2.00	-	0.00	0.00
P46		9.0 MT. WIDE Internal Road	2.00	-	-	-	-	-	2.00	-	0.00	0.00
P47		9.0 MT. WIDE Internal Road	2.00	-	-	-	-	-	2.00	-	0.00	0.00
P48		9.0 MT. WIDE Internal Road	2.00	-	-	-	-	-	2.00	-	0.00	0.00
P49		9.0 MT. WIDE Internal Road	2.00	-	-	-	-	-	2.00	-	0.00	0.00
P49		9.0 MT. WIDE Internal Road	2.00	-	-	-	-	-	-	-	0.00	0.00
P69		9.0 MT. WIDE Internal Road	2.00	-	-	-	-	-	2.00	-	0.00	0.00
P68		9.0 MT. WIDE Internal Road	2.00	-	-	-	-	-	2.00	-	0.00	0.00
P67		9.0 MT. WIDE Internal Road	2.00	-	-	-	-	-	2.00	-	0.00	0.00
P66		9.0 MT. WIDE Internal Road	2.00	-	-	-	-	-	2.00	-	0.00	0.00
P65		9.0 MT. WIDE Internal Road	2.00	-	-	-	-	-	2.00	-	0.00	0.00
P64		9.0 MT. WIDE Internal Road	2.00	-	-	-	-	-	2.00	-	0.00	0.00
P63		9.0 MT. WIDE Internal Road	2.00	-	-	-	-	-	2.00	-	0.00	0.00
P62		9.0 MT. WIDE Internal Road	2.00	-	-	-	-	-	2.00	-	0.00	0.00
P61		9.0 MT. WIDE Internal Road	2.00	-	-	-	-	-	2.00	-	0.00	0.00
P60		9.0 MT. WIDE Internal Road	2.00	-	-	-	-	-	2.00	-	0.00	0.00
P70		9.0 MT. WIDE Internal Road	2.00	-	-	-	-	-	2.00	-	0.00	0.00
P71		9.0 MT. WIDE Internal Road	2.00	-	-	-	-	-	2.00	-	0.00	0.00
P72		9.0 MT. WIDE Internal Road	2.00	-	-	-	-	-	2.00	-	0.00	0.00
P73		9.0 MT. WIDE Internal Road	2.00	-	-	-	-	-	2.00	-	0.00	0.00
P74		9.0 MT. WIDE Internal Road	2.00	-	-	-	-	-	2.00	-	0.00	0.00
P75		9.0 MT. WIDE Internal Road	2.00	-	-	-	-	-	2.00	-	0.00	0.00
P76		9.0 MT. WIDE Internal Road	2.00	-	-	-	-	-	2.00	-	0.00	0.00
P77		9.0 MT. WIDE Internal Road	2.00	-	-	-	-	-	2.00	-	0.00	0.00
P78		9.0 MT. WIDE Internal Road	2.00	-	-	-	-	-	2.00	-	0.00	0.00
P79		9.0 MT. WIDE Internal Road	2.00	-	-	-	-	-	2.00	-	0.00	0.00
P80		9.0 MT. WIDE Internal Road	2.00	-	-	-	-	-	2.00	-	0.00	0.00
P59		9.0 MT. WIDE Internal Road	2.00	-	-	-	-	-	2.00	-	0.00	0.00
P58		9.0 MT. WIDE Internal Road	2.00	-	-	-	-	-	2.00	-	0.00	0.00
P81		9.0 MT. WIDE Internal Road	2.00	-	-	-	-	-	2.00	-	0.00	0.00
P57		9.0 MT. WIDE Internal Road	2.00	-	-	-	-	-	2.00	-	0.00	0.00
P82		9.0 MT. WIDE Internal Road	2.00	-	-	-	-	-	2.00	-	0.00	0.00
P56		9.0 MT. WIDE Internal Road	2.00	-	-	-	-	-	2.00	-	0.00	0.00
P83		9.0 MT. WIDE Internal Road	2.00	-	-	-	-	-	2.00	-	0.00	0.00
P55		9.0 MT. WIDE Internal Road	2.00	-	-	-	-	-	2.00	-	0.00	0.00
P84		9.0 MT. WIDE Internal Road	2.00	-	-	-	-	-	2.00	-	0.00	0.00
P54		9.0 MT. WIDE Internal Road	2.00	-	-	-	-	-	2.00	-	0.00	0.00
P85		9.0 MT. WIDE Internal Road	2.00	-	-	-	-	-	2.00	-	0.00	0.00
P53		9.0 MT. WIDE Internal Road	2.00	-	-	-	-	-	2.00	-	0.00	0.00
P86		9.0 MT. WIDE Internal Road	2.00	-	-	-	-	-	2.00	-	0.00	0.00
P52		9.0 MT. WIDE Internal Road	2.00	-	-	-	-	-	2.00	-	0.00	0.00
P87		9.0 MT. WIDE Internal Road	2.00	-	-	-	-	-	2.00	-	0.00	0.00
P51		9.0 MT. WIDE Internal Road	2.00	-	-	-	-	-	2.00	-	0.00	0.00
P88		9.0 MT. WIDE Internal Road	2.00	-	-	-	-	-	2.00	-	0.00	0.00
P89		9.0 MT. WIDE Internal Road	2.00	-	-	-	-	-	2.00	-	0.00	0.00
P89		9.0 MT. WIDE Internal Road	2.00	-	-	-	-	-	-	-	0.00	0.00
P50		9.0 MT. WIDE Internal Road	2.00	-	-	-	-	-	2.00	-	0.00	0.00
P50		9.0 MT. WIDE Internal Road	2.00	-	-	-	-	-	-	-	0.00	0.00
P118		9.0 MT. WIDE Internal Road	2.00	-	-	-	-	-	2.00	-	0.00	0.00
P117		9.0 MT. WIDE Internal Road	2.00	-	-	-	-	-	2.00	-	0.00	0.00
P116		9.0 MT. WIDE Internal Road	2.00	-	-	-	-	-	2.00	-	0.00	0.00
P115		9.0 MT. WIDE Internal Road	2.00	-	-	-	-	-	2.00	-	0.00	0.00
P114		9.0 MT. WIDE Internal Road	2.00	-	-	-	-	-	2.00	-	0.00	0.00
P114		9.0 MT. WIDE Internal Road	2.00	-	-	-	-	-	-	-	0.00	0.00
P121		9.0 MT. WIDE Internal Road	2.00	-	-	-	-	-	2.00	-	0.00	0.00
P121		9.0 MT. WIDE Internal Road	2.00	-	-	-	-	-	-	-	0.00	0.00
P120		9.0 MT. WIDE Internal Road	2.00	-	-	-	-	-	2.00	-	0.00	0.00
P119		9.0 MT. WIDE Internal Road	2.00	-	-	-	-	-	2.00	-	0.00	0.00
P122		9.0 MT. WIDE Internal Road	2.00	-	-	-	-	-	2.00	-	0.00	0.00
P122		9.0 MT. WIDE Internal Road	2.00	-	-	-	-	-	-	-	0.00	0.00
P113		9.0 MT. WIDE Internal Road	2.00	-	-	-	-	-	2.00	-	0.00	0.00
P113		9.0 MT. WIDE Internal Road	2.00	-	-	-	-	-	-	-	0.00	0.00
P112		9.0 MT. WIDE Internal Road	2.00	-	-	-	-	-	2.00	-	0.00	0.00
P123		9.0 MT. WIDE Internal Road	2.00	-	-	-	-	-	2.00	-	0.00	0.00
P111		9.0 MT. WIDE Internal Road	2.00	-	-	-	-	-	2.00	-	0.00	0.00
P124		9.0 MT. WIDE Internal Road	2.00	-	-	-	-	-	2.00	-	0.00	0.00
P110		9.0 MT. WIDE Internal Road	2.00	-	-	-	-	-	2.00	-	0.00	0.00
P125		9.0 MT. WIDE Internal Road	2.00	-	-	-	-	-	2.00	-	0.00	0.00
P109		9.0 MT. WIDE Internal Road	2.00	-	-	-	-	-	2.00	-	0.00	0.00
P126		9.0 MT. WIDE Internal Road	2.00	-	-	-	-	-	2.00	-	0.00	0.00
P108		9.0 MT. WIDE Internal Road	2.00	-	-	-	-	-	2.00	-	0.00	0.00
P127		9.0 MT. WIDE Internal Road	2.00	-	-	-	-	-	2.00	-	0.00	0.00
P107		9.0 MT. WIDE Internal Road	2.00	-	-	-	-	-	2.00	-	0.00	0.00
P128		9.0 MT. WIDE Internal Road	2.00	-	-	-	-	-	2.00	-	0.00	0.00
P106		9.0 MT. WIDE Internal Road	2.00	-	-	-	-	-	2.00	-	0.00	0.00
P129		9.0 MT. WIDE Internal Road	2.00	-	-	-	-	-	2.00	-	0.00	0.00
P105		9.0 MT. WIDE Internal Road	2.00	-	-	-	-	-	2.00	-	0.00	0.00
P130		9.0 MT. WIDE Internal Road	2.00	-	-	-	-	-	2.00	-	0.00	0.00
P104		9.0 MT. WIDE Internal Road	2.00	-	-	-	-	-	2.00	-	0.00	0.00
P131		9.0 MT. WIDE Internal Road	2.00	-	-	-	-	-	2.00	-	0.00	0.00
P103		9.0 MT. WIDE Internal Road	2.00	-	-	-	-	-	2.00	-	0.00	0.00
P132		9.0 MT. WIDE Internal Road	2.00	-	-	-	-	-	2.00	-	0.00	0.00
P102		9.0 MT. WIDE Internal Road	2.00	-	-	-	-	-	2.00	-	0.00	0.00
P133		9.0 MT. WIDE Internal Road	2.00	-	-	-	-	-	2.00	-	0.00	0.00
P101		9.0 MT. WIDE Internal Road	2.00	-	-	-	-	-	2.00	-	0.00	0.00
P134		9.0 MT. WIDE Internal Road	2.00	-	-	-	-	-	2.00	-	0.00	0.00
P100		9.0 MT. WIDE Internal Road	2.00	-	-	-	-	-	2.00	-	0.00	0.00
P135		9.0 MT. WIDE Internal Road	2.00	-	-	-	-	-	2.00	-	0.00	0.00
P99		9.0 MT. WIDE Internal Road	2.00	-	-	-	-	-	2.00	-	0.00	0.00
P136		9.0 MT. WIDE Internal Road	2.00	-	-	-	-	-	2.00	-	0.00	0.00
P98		9.0 MT. WIDE Internal Road	2.00	-	-	-	-	-	2.00	-	0.00	0.00
P137		9.0 MT. WIDE Internal Road	2.00	-	-	-	-	-	2.00	-	0.00	0.00
P97		9.0 MT. WIDE Internal Road	2.00	-	-	-	-	-	2.00	-	0.00	0.00
P138		9.0 MT. WIDE Internal Road	2.00	-	-	-	-	-	2.00	-	0.00	0.00
P96		9.0 MT. WIDE Internal Road	2.00	-	-	-	-	-	2.00	-	0.00	0.00
P139		9.0 MT. WIDE Internal Road	2.00	-	-	-	-	-	2.00	-	0.00	0.00
P95		9.0 MT. WIDE Internal Road	2.00	-	-	-	-	-	2.00	-	0.00	0.00
P140		9.0 MT. WIDE Internal Road	2.00	-	-	-	-	-	2.00	-	0.00	0.00
P94		9.0 MT. WIDE Internal Road	2.00	-	-	-	-	-	2.00	-	0.00	0.00
P141		9.0 MT. WIDE Internal Road	2.00	-	-	-	-	-	2.00	-	0.00	0.00
P93		9.0 MT. WIDE Internal Road	2.00	-	-	-	-	-	2.00	-	0.00	0.00
P142		9.0 MT. WIDE Internal Road	2.00	-	-	-	-	-	2.00	-	0.00	0.00
P92		9.0 MT. WIDE Internal Road	2.00	-	-	-	-	-	2.00	-	0.00	0.00
P143		9.0 MT. WIDE Internal Road	2.00	-	-	-	-	-	2.00	-	0.00	0.00
P91		9.0 MT. WIDE Internal Road	2.00	-	-	-	-	-	2.00	-	0.00	0.00
P144		9.0 MT. WIDE Internal Road	2.00	-	-	-	-	-	2.00	-	0.00	0.00
P90		9.0 MT. WIDE Internal Road	2.00	-	-	-	-	-	2.00	-	0.00	0.00
P90		9.0 MT. WIDE Internal Road	2.00	-	-	-	-	-	-	-	0.00	0.00
P145		9.0 MT. WIDE Internal Road	2.00	-	-	-	-	-	2.00	-	0.00	0.00
P145		9.0 MT. WIDE Internal Road	2.00	-	-	-	-	-	-	-	0.00	0.00
P164		9.0 MT. WIDE Internal Road	3.00	-	-	-	-	-	3.00	-	0.00	0.00
P165		9.0 MT. WIDE Internal Road	3.00	-	-	-	-	-	3.00	-	0.00	0.00
P162		9.0 MT. WIDE Internal Road	3.00	-	-	-	-	-	3.00	-	0.00	0.00
P163		9.0 MT. WIDE Internal Road	3.00	-	-	-	-	-	3.00	-	0.00	0.00
P160		9.0 MT. WIDE Internal Road	3.00	-	-	-	-	-	3.00	-	0.00	0.00
P161		9.0 MT. WIDE Internal Road	3.00	-	-	-	-	-	3.00	-	0.00	0.00
P158		9.0 MT. WIDE Internal Road	3.00	-	-	-	-	-	3.00	-	0.00	0.00
P159		9.0 MT. WIDE Internal Road	3.00	-	-	-	-	-	3.00	-	0.00	0.00
P156		9.0 MT. WIDE Internal Road	3.00	-	-	-	-	-	3.00	-	0.00	0.00
P157		9.0 MT. WIDE Internal Road	3.00	-	-	-	-	-	3.00	-	0.00	0.00
P154		9.0 MT. WIDE Internal Road	3.00	-	-	-	-	-	3.00	-	0.00	0.00
P155		9.0 MT. WIDE Internal Road	3.00	-	-	-	-	-	3.00	-	0.00	0.00
P152		9.0 MT. WIDE Internal Road	3.00	-	-	-	-	-	3.00	-	0.00	0.00
P153		9.0 MT. WIDE Internal Road	3.00	-	-	-	-	-	3.00	-	0.00	0.00
P150		9.0 MT. WIDE Internal Road	3.00	-	-	-	-	-	3.00	-	0.00	0.00
P151		9.0 MT. WIDE Internal Road	3.00	-	-	-	-	-	3.00	-	0.00	0.00
P182		9.0 MT. WIDE Internal Road	3.00	-	-	-	-	-	3.00	-	0.00	0.00
P182		9.0 MT. WIDE Internal Road	3.00	-	-	-	-	-	-	-	0.00	0.00
P149		9.0 MT. WIDE Internal Road	3.00	-	-	-	-	-	3.00	-	0.00	0.00
P149		9.0 MT. WIDE Internal Road	3.00	-	-	-	-	-	-	-	0.00	0.00
P180		9.0 MT. WIDE Internal Road	3.00	-	-	-	-	-	3.00	-	0.00	0.00
P181		9.0 MT. WIDE Internal Road	3.00	-	-	-	-	-	3.00	-	0.00	0.00
P178		9.0 MT. WIDE Internal Road	3.00	-	-	-	-	-	3.00	-	0.00	0.00
P179		9.0 MT. WIDE Internal Road	3.00	-	-	-	-	-	3.00	-	0.00	0.00
P176		9.0 MT. WIDE Internal Road	3.00	-	-	-	-	-	3.00	-	0.00	0.00
P177		9.0 MT. WIDE Internal Road	3.00	-	-	-	-	-	3.00	-	0.00	0.00
P175		9.0 MT. WIDE Internal Road	3.00	-	-	-	-	-	3.00	-	0.00	0.00
P173		9.0 MT. WIDE Internal Road	3.00	-	-	-	-	-	3.00	-	0.00	0.00
P174		9.0 MT. WIDE Internal Road	3.00	-	-	-	-	-	3.00	-	0.00	0.00
P172		9.0 MT. WIDE Internal Road	3.00	-	-	-	-	-	3.00	-	0.00	0.00
P171		9.0 MT. WIDE Internal Road	3.00	-	-	-	-	-	3.00	-	0.00	0.00
P170		9.0 MT. WIDE Internal Road	3.00	-	-	-	-	-	3.00	-	0.00	0.00
P169		9.0 MT. WIDE Internal Road	3.00	-	-	-	-	-	3.00	-	0.00	0.00
P166		9.0 MT. WIDE Internal Road	3.00	-	-	-	-	-	3.00	-	0.00	0.00
P167		9.0 MT. WIDE Internal Road	3.00	-	-	-	-	-	3.00	-	0.00	0.00
P168		9.0 MT. WIDE Internal Road	3.00	-	-	-	-	-	3.00	-	0.00	0.00
P183		9.0 MT. WIDE Internal Road	2.00	-	-	-	-	-	2.00	-	0.00	0.00
P184		9.0 MT. WIDE Internal Road	2.00	-	-	-	-	-	2.00	-	0.00	0.00
P186		9.0 MT. WIDE Internal Road	2.00	-	-	-	-	-	2.00	-	0.00	0.00
P185		9.0 MT. WIDE Internal Road	2.00	-	-	-	-	-	2.00	-	0.00	0.00
P188		9.0 MT. WIDE Internal Road	2.00	-	-	-	-	-	2.00	-	0.00	0.00
P187		9.0 MT. WIDE Internal Road	2.00	-	-	-	-	-	2.00	-	0.00	0.00
P190		9.0 MT. WIDE Internal Road	2.00	-	-	-	-	-	2.00	-	0.00	0.00
P189		9.0 MT. WIDE Internal Road	2.00	-	-	-	-	-	2.00	-	0.00	0.00
P191		9.0 MT. WIDE Internal Road	2.00	-	-	-	-	-	2.00	-	0.00	0.00
P192		9.0 MT. WIDE Internal Road	2.00	-	-	-	-	-	-	-	0.00	0.00
P147		9.0 MT. WIDE Internal Road	4.50	-	-	-	-	-	4.50	-	0.00	0.00
P148		9.0 MT. WIDE Internal Road	4.50	-	-	-	-	-	4.50	-	0.00	0.00
P148		9.0 MT. WIDE Internal Road	4.50	-	-	-	-	-	-	-	0.00	0.00
P146		9.0 MT. WIDE Internal Road	4.50	-	-	-	-	-	4.50	-	0.00	0.00

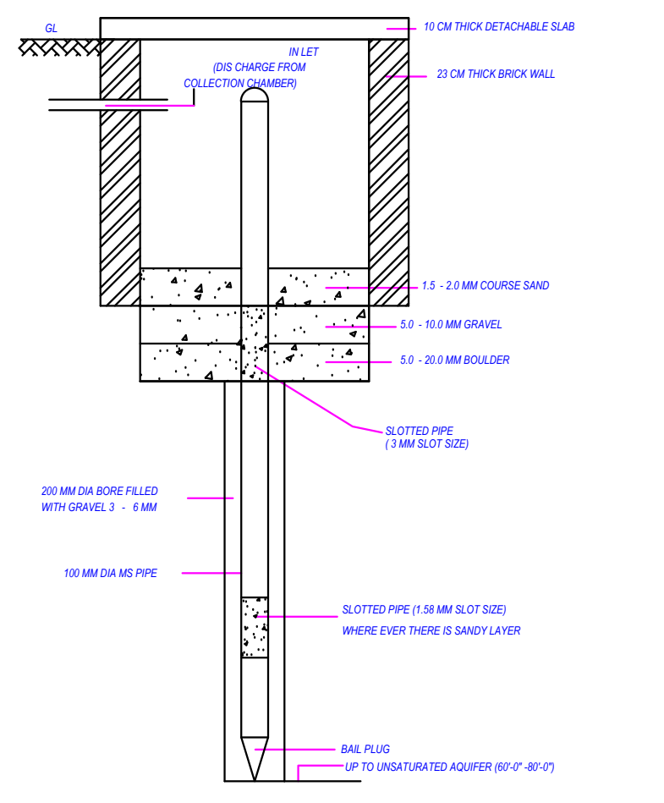

RAIN WATER HARVESTING DETAIL

[NOT TO SCALE]

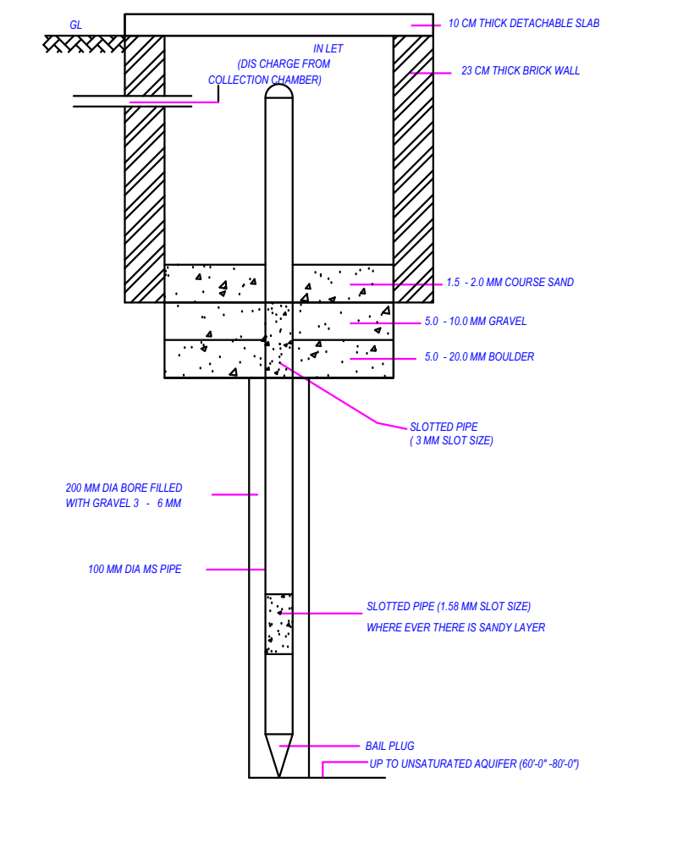

PERCOLATION WELL DETAILS

[NOT TO SCALE]

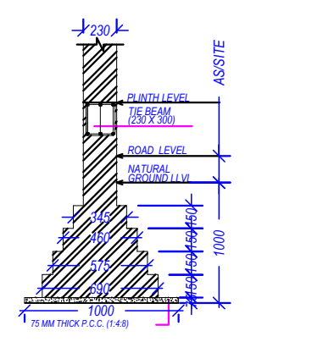

FOUNDATION DETAIL

[AS PER STRUCTURE DRG.]

(NOT TO SCALE)

OWNER'S NAME AND SIGNATURE	
PARDOUS DEVELOPERS PVT LTD, jschawla@ctc-lid.com, 9810571165	
ARCH/ENG'S NAME AND SIGNA	UCTURE ENGINEER
Rajneesh Kumar CA/2017/86949 Signature Not Verified Digitally signed by Rajneesh Kumar Date: 22 Dec 2023 10:49:35 Designation :Architect	Lucknow Development Authority
	Signature Not Verified Digitally signed by INDRA MANI TRIPATHI Date: 22 Dec 2023 19:21:14 Organization :Lucknow Development Authority Designation :Vice Chairman

Building Plan Application Number

LDA/LD/23-24/3009

Sanctioned On

15 Dec 2023

Valid Till

21 Dec 2028

Approved By

Vice Chairman (Vice Chairman)

Examined By

Lakshman Singh (Junior engineer)

Atul Sharma (Junior engineer)

Rajesh Sharma (Assistant Engineer)

Atul Sharma (Junior engineer)

Rajesh Sharma (Assistant Engineer)

Atul Sharma (Junior engineer)

Note: - 1) This drawing is prepared as per the current prevailing Building Bye Laws.
2) If Map sanctioned is used for purpose anything other than stated in application will lead to rejection of Map.

Total Plot Area: -	46492.21	Total FAR Area: -	0.00
Total Coverage Area: -	0.00	Total BUA Area: -	0.00

The correctness and accuracy of Proposal Information and drawing is a responsibility of POR/owner. Accuracy of Scrutiny Report is subject to accuracy of end-user provided data, 3rd party software/hardware/services, etc. SoftTech Engineers Ltd. is not liable for any damages which may arise from use, or inability to use the Application. Texts printed in 'Italics' and 'Blue' color are user inputs, which are not verified and not generated by scrutiny software.

Project Title : REVISED SUBMISSION DRG FOR THE MAP NO-LDA/LD/22-23/2397 LAY OUT PLOTTED DEVELOPMENT FOR PLOT NO:- GH-3, SECTOR -H, HIGH TECH TOWNSHIP , SUSHANT GOLF CITY , LUCKNOWOWNER :- M/S PARDOS DEVELOPERS PVT. LTD.

File No	LDA/LD/23-24/3009	Sheet	3 / 4
Submission Date	2023-11-17	Scale	1:100

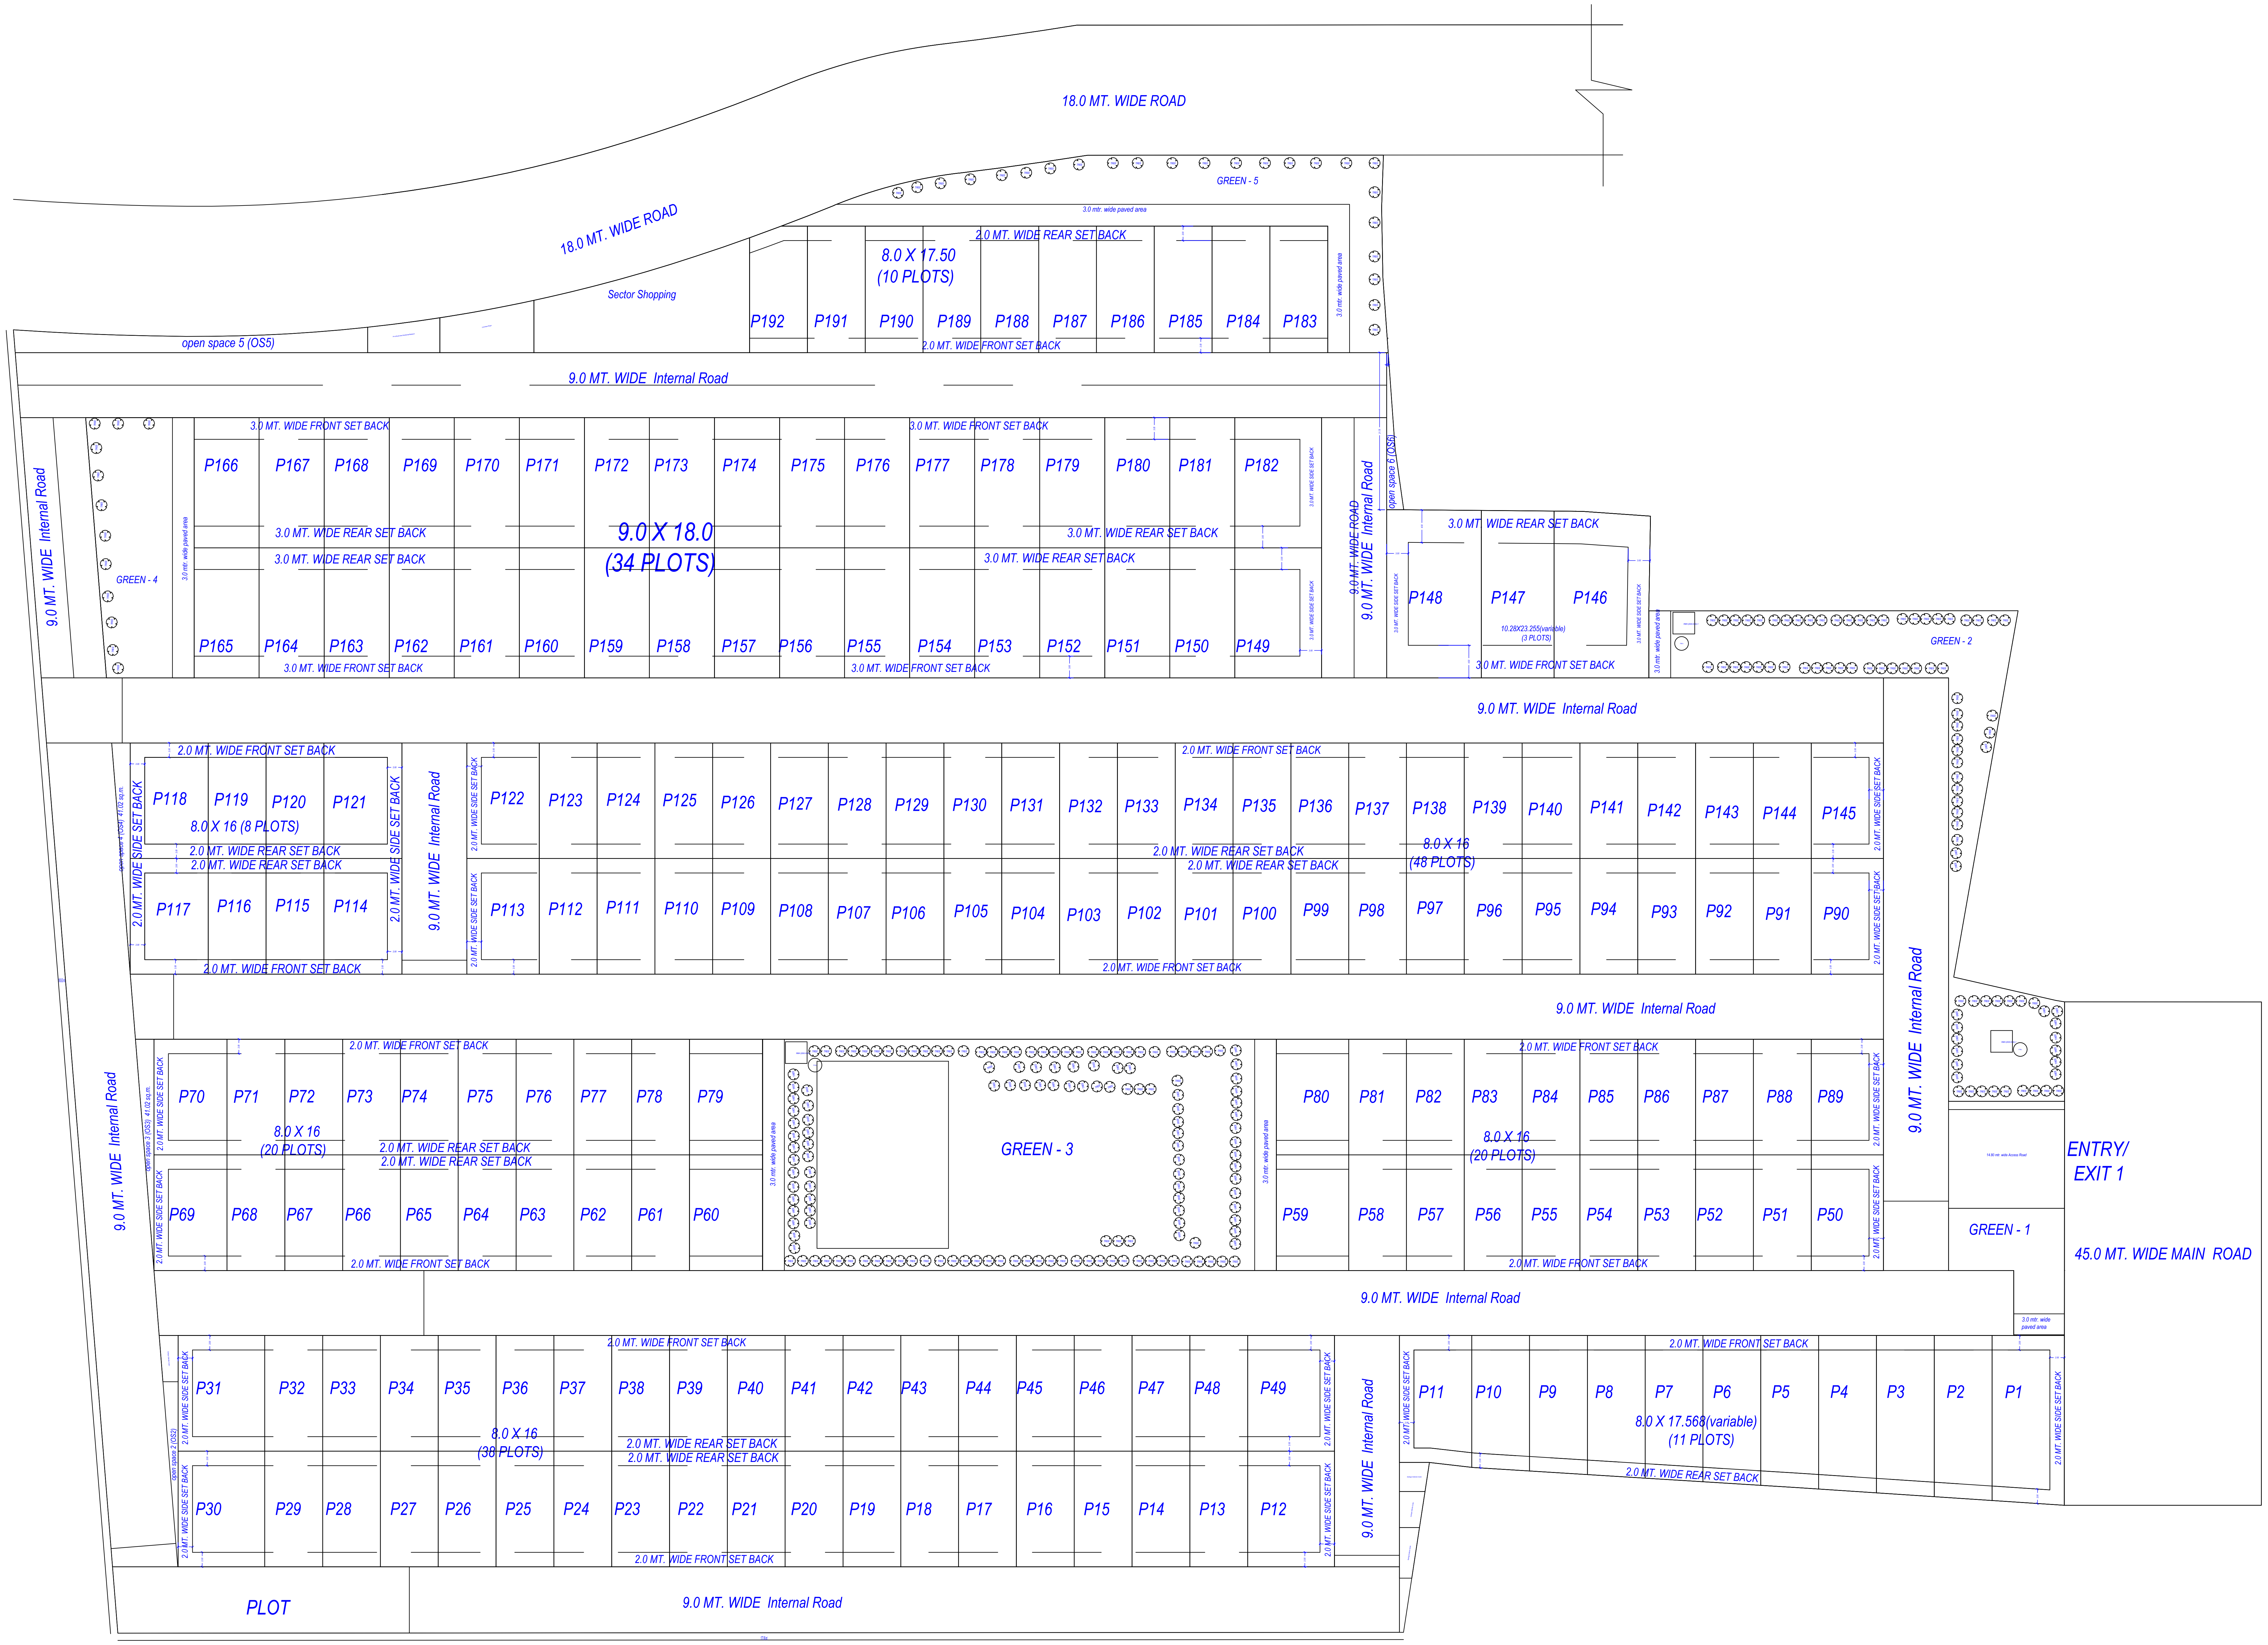
18.0 MT. WIDE ROAD
18.0 MT. WIDE ROAD
Sector Shopping
open space 5 (OS5)
GREEN - 5
3.0 mtr. wide paved area
8.0 X 17.50
(10 PLOTS)
2.0 MT. WIDE REAR SET BACK
2.0 MT. WIDE FRONT SET BACK
9.0 MT. WIDE Internal Road
3.0 MT. WIDE FRONT SET BACK
3.0 MT. WIDE REAR SET BACK
9.0 X 18.0
(34 PLOTS)
GREEN - 4
9.0 MT. WIDE Internal Road
open space 6 (OS6)
10.26X23.255(variable)
(3 PLOTS)
GREEN - 2
8.0 X 16 (8 PLOTS)
2.0 MT. WIDE SIDE SET BACK
8.0 X 16
(48 PLOTS)
8.0 X 16
(20 PLOTS)
GREEN - 3
8.0 X 16
(20 PLOTS)
ENTRY/
EXIT 1
GREEN - 1
45.0 MT. WIDE MAIN ROAD
8.0 X 16
(38 PLOTS)
8.0 X 17.568(variable)
(11 PLOTS)
PLOT
P1
P192

SERVICE PLAN

OWNER'S NAME AND SIGNATURE	
PARDOUS DEVELOPERS PVT LTD, jschawla@ctc-lid.com, 9810571165	
ARCH/ENG'S NAME AND SIGNA	UCTURE ENGINEER
Rajneesh Kumar CA/2017/86949	
Signature Not Verified Digitally signed by Rajneesh Kumar Date: 22 Dec 2023 10:49:35 Designation :Architect	Lucknow Development Authority
	Signature Not Verified Digitally signed by INDRA MANI TRIPATHI Date: 22 Dec 2023 19:21:14 Organization :Lucknow Development Authority Designation :Vice Chairman

Building Plan Application Number
LDA/LD/23-24/3009

Sanctioned On
15 Dec 2023

Valid Till
21 Dec 2028

Approved By
Vice Chairman (Vice Chairman)

Examined By
Lakshman Singh (Junior engineer)

Atul Sharma (Junior engineer)

Rajesh Sharma (Assistant Engineer)

Atul Sharma (Junior engineer)

Rajesh Sharma (Assistant Engineer)

Atul Sharma (Junior engineer)

Note: - 1) This drawing is prepared as per the current prevailing Building Bye Laws.
2) If Map sanctioned is used for purpose anything other than stated in application will lead to rejection of Map.

Total Plot Area: -	46492.21	Total FAR Area: -	0.00
Total Coverage Area: -	0.00	Total BUA Area: -	0.00

ISO_A0_(841.00_x_1189.00_MM)

The correctness and accuracy of Proposal Information and drawing is a responsibilty of POR/owner. Accuracy of Scrutiny Report is subject to accuracy of end-user provided data, 3rd party software/hardware/services, etc. SoftTech Engineers Ltd. is not liable for any damages which may arise from use, or inability to use the Application. Texts printed in 'Italics' and 'Blue' color are user inputs, which are not verified and not generated by scrutiny software.

Project Title : REVISED SUBMISSION DRG FOR THE MAP NO-LDA/LD/22-23/2397 LAY OUT PLOTTED DEVELOPMENT FOR PLOT NO:- GH-3, SECTOR -H, HIGH TECH TOWNSHIP , SUSHANT GOLF CITY , LUCKNOWOWNER :- M/S PARDOS DEVELOPERS PVT. LTD.

File No	LDA/LD/23-24/3009	Sheet	4 / 4
Submission Date	2023-11-17	Scale	1:100

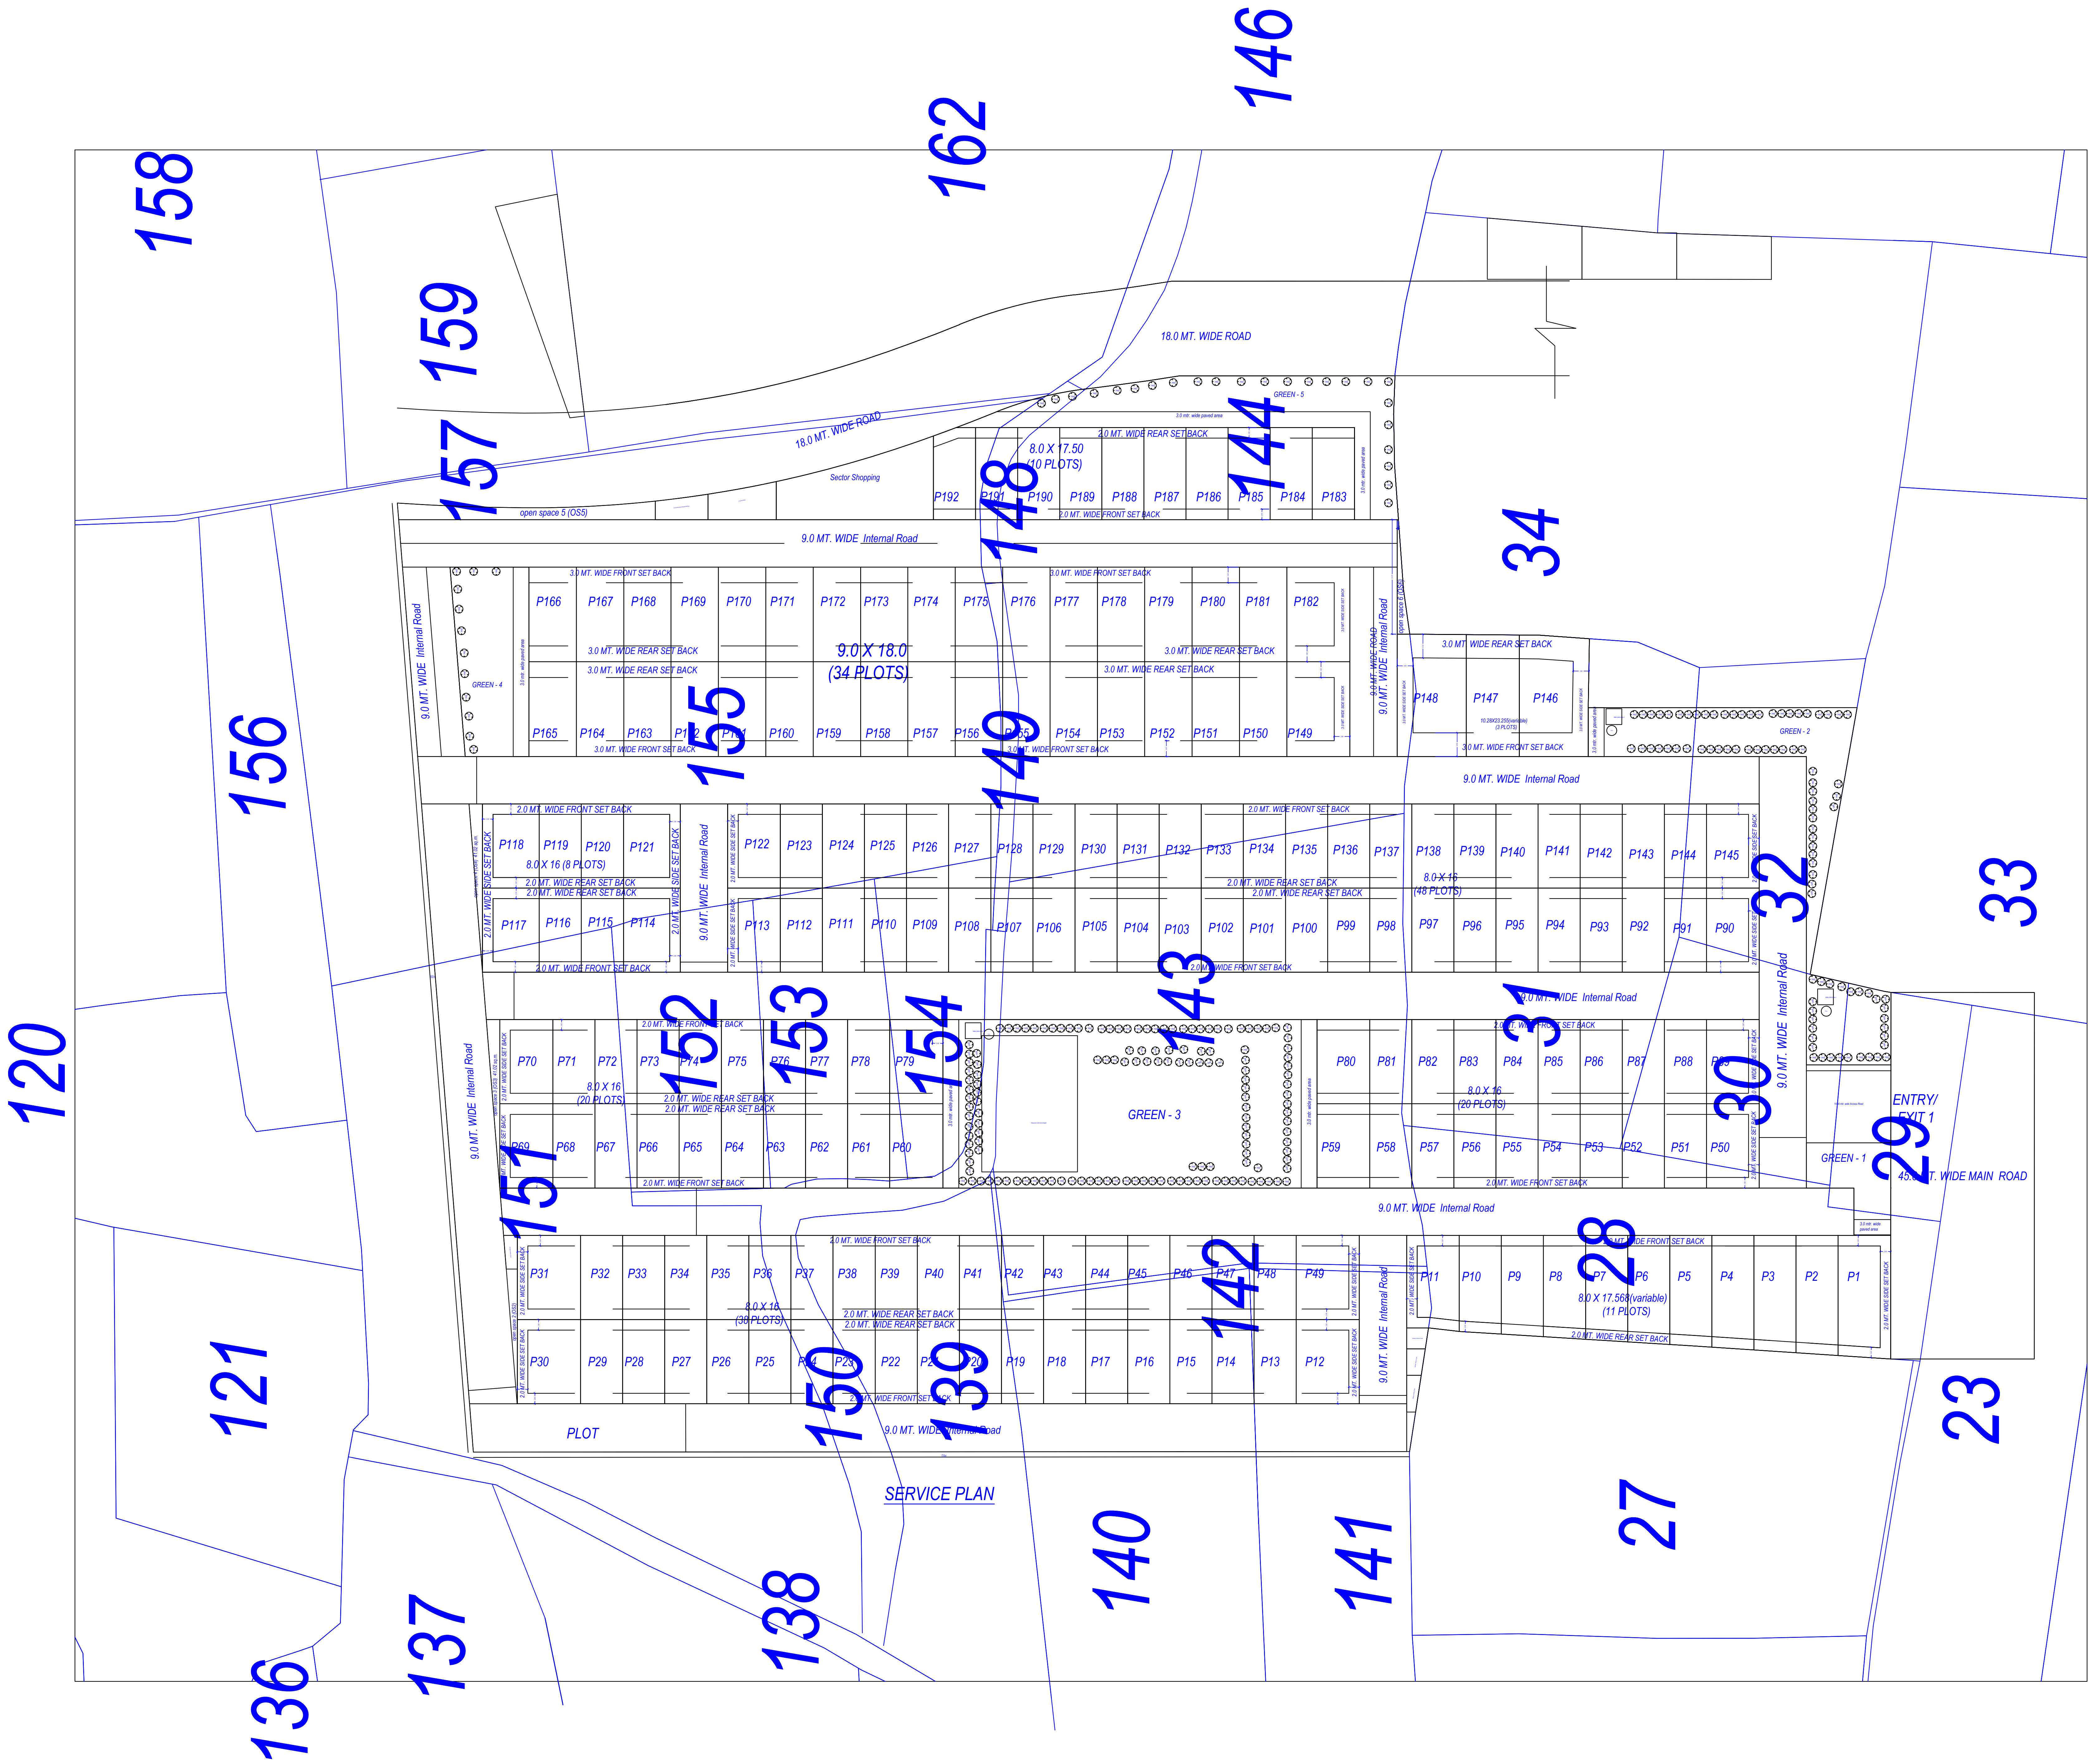
146
162
158
159
157
18.0 MT. WIDE ROAD
18.0 MT. WIDE ROAD
Sector Shopping
open space 5 (OSS)
GREEN - 5
3.0 MT. WIDE REAR SET BACK
8.0 X 17.50
(10 PLOTS)
P192
P191
P190
P189
P188
P187
P186
P185
P184
P183
3.0 MT. WIDE FRONT SET BACK
144
148
34
9.0 MT. WIDE Internal Road
3.0 MT. WIDE FRONT SET BACK
P166
P167
P168
P169
P170
P171
P172
P173
P174
P175
P176
P177
P178
P179
P180
P181
P182
3.0 MT. WIDE REAR SET BACK
9.0 X 18.0
(34 PLOTS)
P165
P164
P163
P160
P159
P158
P157
P156
P154
P153
P152
P151
P150
P149
GREEN - 4
9.0 MT. WIDE Internal Road
156
155
149
3.0 MT. WIDE REAR SET BACK
P148
P147
P146
GREEN - 2
9.0 MT. WIDE Internal Road
2.0 MT. WIDE FRONT SET BACK
P118
P119
P120
P121
8.0 X 16 (8 PLOTS)
2.0 MT. WIDE REAR SET BACK
P117
P116
P115
P114
P122
P123
P124
P125
P126
P127
P128
P129
P130
P131
P132
P133
P134
P135
P136
P137
P138
P139
P140
P141
P142
P143
P144
P145
8.0 X 16
(45 PLOTS)
P113
P112
P111
P110
P109
P108
P107
P106
P105
P104
P103
P102
P101
P100
P99
P98
P97
P96
P95
P94
P93
P92
P91
P90
32
33
120
9.0 MT. WIDE Internal Road
143
31
153
152
154
P70
P71
P72
P73
P74
P75
P76
P77
P78
P79
8.0 X 16
(20 PLOTS)
P69
P68
P67
P66
P65
P64
P63
P62
P61
P60
GREEN - 3
P80
P81
P82
P83
P84
P85
P86
P87
P88
P89
8.0 X 16
(20 PLOTS)
P59
P58
P57
P56
P55
P54
P53
P52
P51
P50
30
ENTRY/
EXIT 1
29
GREEN - 1
45.0 MT. WIDE MAIN ROAD
151
9.0 MT. WIDE Internal Road
3.0 MT. WIDE FRONT SET BACK
P31
P32
P33
P34
P35
P36
P37
P38
P39
P40
P41
P42
P43
P44
P45
P46
P47
P48
P49
8.0 X 16
(38 PLOTS)
2.0 MT. WIDE REAR SET BACK
P30
P29
P28
P27
P26
P25
P24
P23
P22
P21
P20
P19
P18
P17
P16
P15
P14
P13
P12
142
150
139
28
P11
P10
P9
P8
P7
P6
P5
P4
P3
P2
P1
8.0 X 17.56(variable)
(11 PLOTS)
2.0 MT. WIDE REAR SET BACK
9.0 MT. WIDE Internal Road
PLOT
9.0 MT. WIDE Internal Road
SERVICE PLAN
121
23
27
140
141
138
137
136

LANDSCAPE PLAN

OWNER'S NAME AND SIGNATURE

PARDOUS DEVELOPERS PVT LTD, jschawla@ctc-lid.com, 9810571165

ARCH/ENG'S NAME AND SIGNA UCTURE ENGINEER

Rajneesh Kumar

CA/2017/86949

Signature Not Verified
Digitally signed by Rajneesh Kumar
Date: 22 Dec 2023 10:49:35
Designation :Architect

Lucknow Development Authority

Signature Not Verified
Digitally signed by INDRA MANI TRIPATHI
Date: 22 Dec 2023 19:21:14
Organization :Lucknow Development Authority
Designation :Vice Chairman

Building Plan Application Number
LDA/LD/23-24/3009

Sanctioned On
15 Dec 2023

Valid Till
21 Dec 2028

Approved By
Vice Chairman (Vice Chairman)

Examined By
Lakshman Singh (Junior engineer)
Atul Sharma (Junior engineer)
Rajesh Sharma (Assistant Engineer)
Atul Sharma (Junior engineer)
Rajesh Sharma (Assistant Engineer)
Atul Sharma (Junior engineer)

Note: - 1) This drawing is prepared as per the current prevailing Building Bye Laws.
2) If Map sanctioned is used for purpose anything other than stated in application will lead to rejection of Map.

Total Plot Area: -	46492.21	Total FAR Area: -	0.00
Total Coverage Area: -	0.00	Total BUA Area: -	0.00

ISO_A0_(841.00_x_1189.00_MM)

The correctness and accuracy of Proposal Information and drawing is a responsibilty of POR/owner. Accuracy of Scrutiny Report is subject to accuracy of end-user provided data, 3rd party software/hardware/services, etc. SoftTech Engineers Ltd. is not liable for any damages which may arise from use, or inability to use the Application. Texts printed in 'Italics' and 'Blue' color are user inputs, which are not verified and not generated by scrutiny software.